



PROYECTO

MAHUIDA

EL BOLSÓN - LAGO PUELO / COMARCA ANDINA - PATAGONIA - ARGENTINA



el sol de frente
ciclo de luz y sombras
sobre mahuida

MEMORIA DESCRIPTIVA

La vivienda unifamiliar se concibe como una pieza integrada a la topografía, construida con materiales propios del territorio: tierra, piedra y madera. Se desarrolla en dos plantas. En ambas plantas hay un sector social y otro privado.

Planta baja área social (Estar, Comedor y Cocina), junto con un área privada con 2 dormitorios y servicios.

En planta alta áreas social (Biblioteca, Estudio) conformadas por dormitorios, baños y un estudio.

Los tabiques portantes tipo tapia se apoyan sobre fundaciones ciclópeas. Estos elementos construyen la luz y organizan las visuales, abiertas hacia el norte y protegidas hacia el sur. La estructura de los planos horizontales que definen los niveles se resuelve en madera, al igual que las aberturas con DVH, manteniendo la coherencia material con el entorno. La cubierta modular combina sectores de techo verde y paneles de teja pizarra, logrando una integración natural con el relieve.

El proyecto incorpora sistemas sustentables que refuerzan el vínculo con el entorno: captación solar térmica y fotovoltaica, recolección de aguas de lluvia y tratamiento natural de aguas grises y negras mediante bio filtros vegetales, con descarga hacia el suelo. el agua de lluvias se recolecta en tanques y también se deriva a la pileta tipo laguna natural. La vivienda busca habitar el paisaje con respeto y simpleza, ofreciendo un refugio eficiente y sereno, en armonía con su ambiente natural.

PROGRAMA

Superficie Total: 265 metros cuadrados.




RECIBIDOR / CUARTO FRIO
DESPENSA
LAVADERO
COCINA
COMEDOR
LIVING
PARRILLA Y DUCHA EXTERIOR
DORMITORIO 1
BAÑO 1 (TOILETTE)
DORMITORIO 2 (SUITE PB)
BAÑO 2 (SUITE PB)
ESCRITORIO
ESTUDIO
BIBLIOTECA
DORMITORIO 3 (SUITE PA)
BAÑO 3 (SUITE PA)
VESTIDOR

Instalaciones Tradicionales:

- Provisión tradicional de red de agua.
- Electricidad.
- Sistema de cloacas.


Sistemas e Instalaciones Sustentables:


- **Energía Solar:**
 - o Paneles fotovoltaicos para recolección, acumulación y entrega de energía a la red.
 - o Colectores solares para calefacción de agua, proporcionando agua caliente a los baños y a las y murales radiantes.
- **Control de Aire:**
 - o Inyección de aire controlado de temperatura por pozo canadienses.
 - o Extracción de aire por ventanales superiores.
- Calefacción : Salamandras / hogares a leñas
- Pileta natural con fotofiltros y agua libre de cloro y sintéticos
- **Tratamiento y Reutilización de Aguas:**
 - o Sistema contra incendio.
 - o Tratamiento y reutilización de aguas grises para riego.
 - o Filtrado de aguas negras y grises en pozos fitosanitarios y filtrantes para ser utilizadas en riego o devueltas a las cloacas filtradas.
 - o Recolección de agua de lluvia para riego y servicios no requeridos de agua potable ni consumo humano.
- **Espacios Verdes:**
 - o Amplio ajardinamiento y huertas interiores y en balcones.
 - o Terraza verde

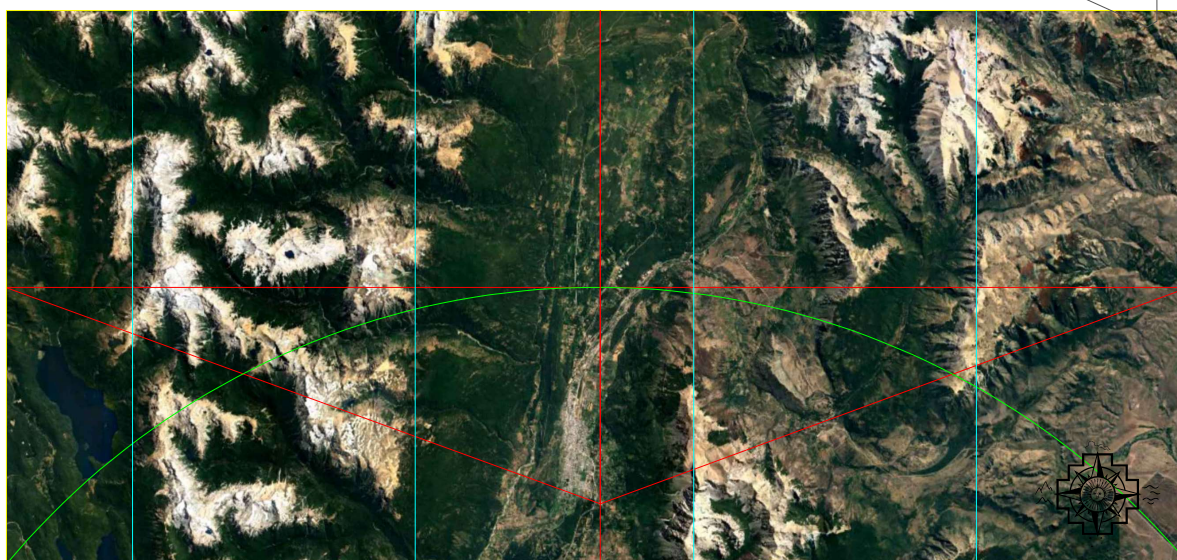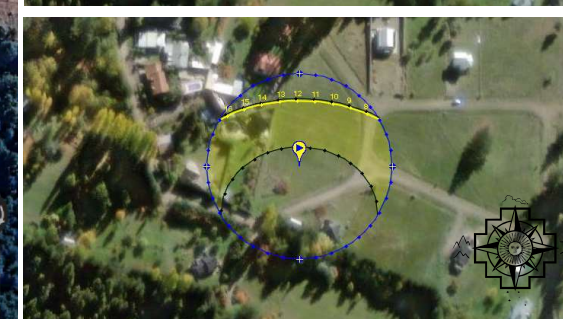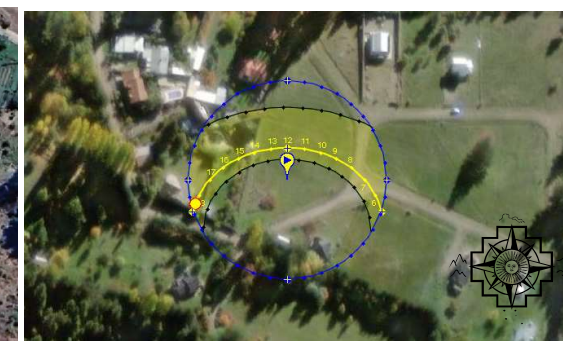








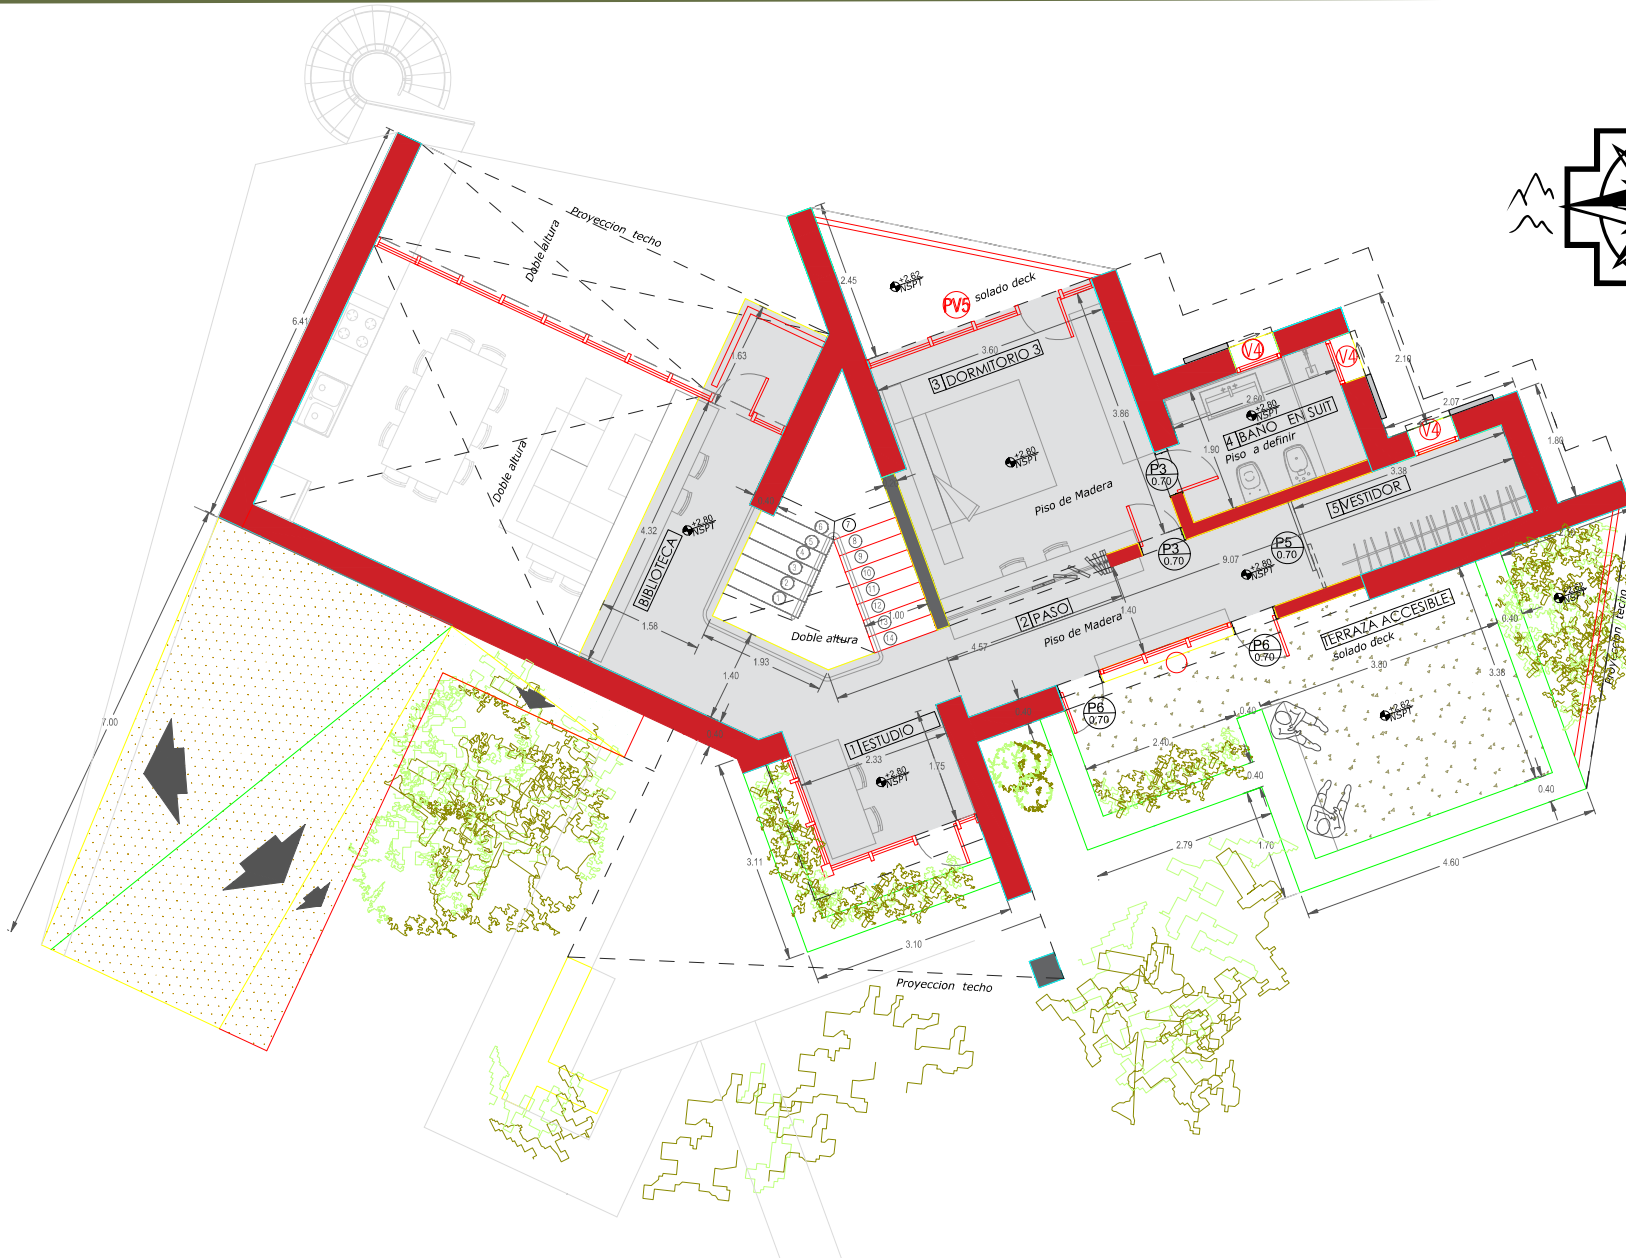


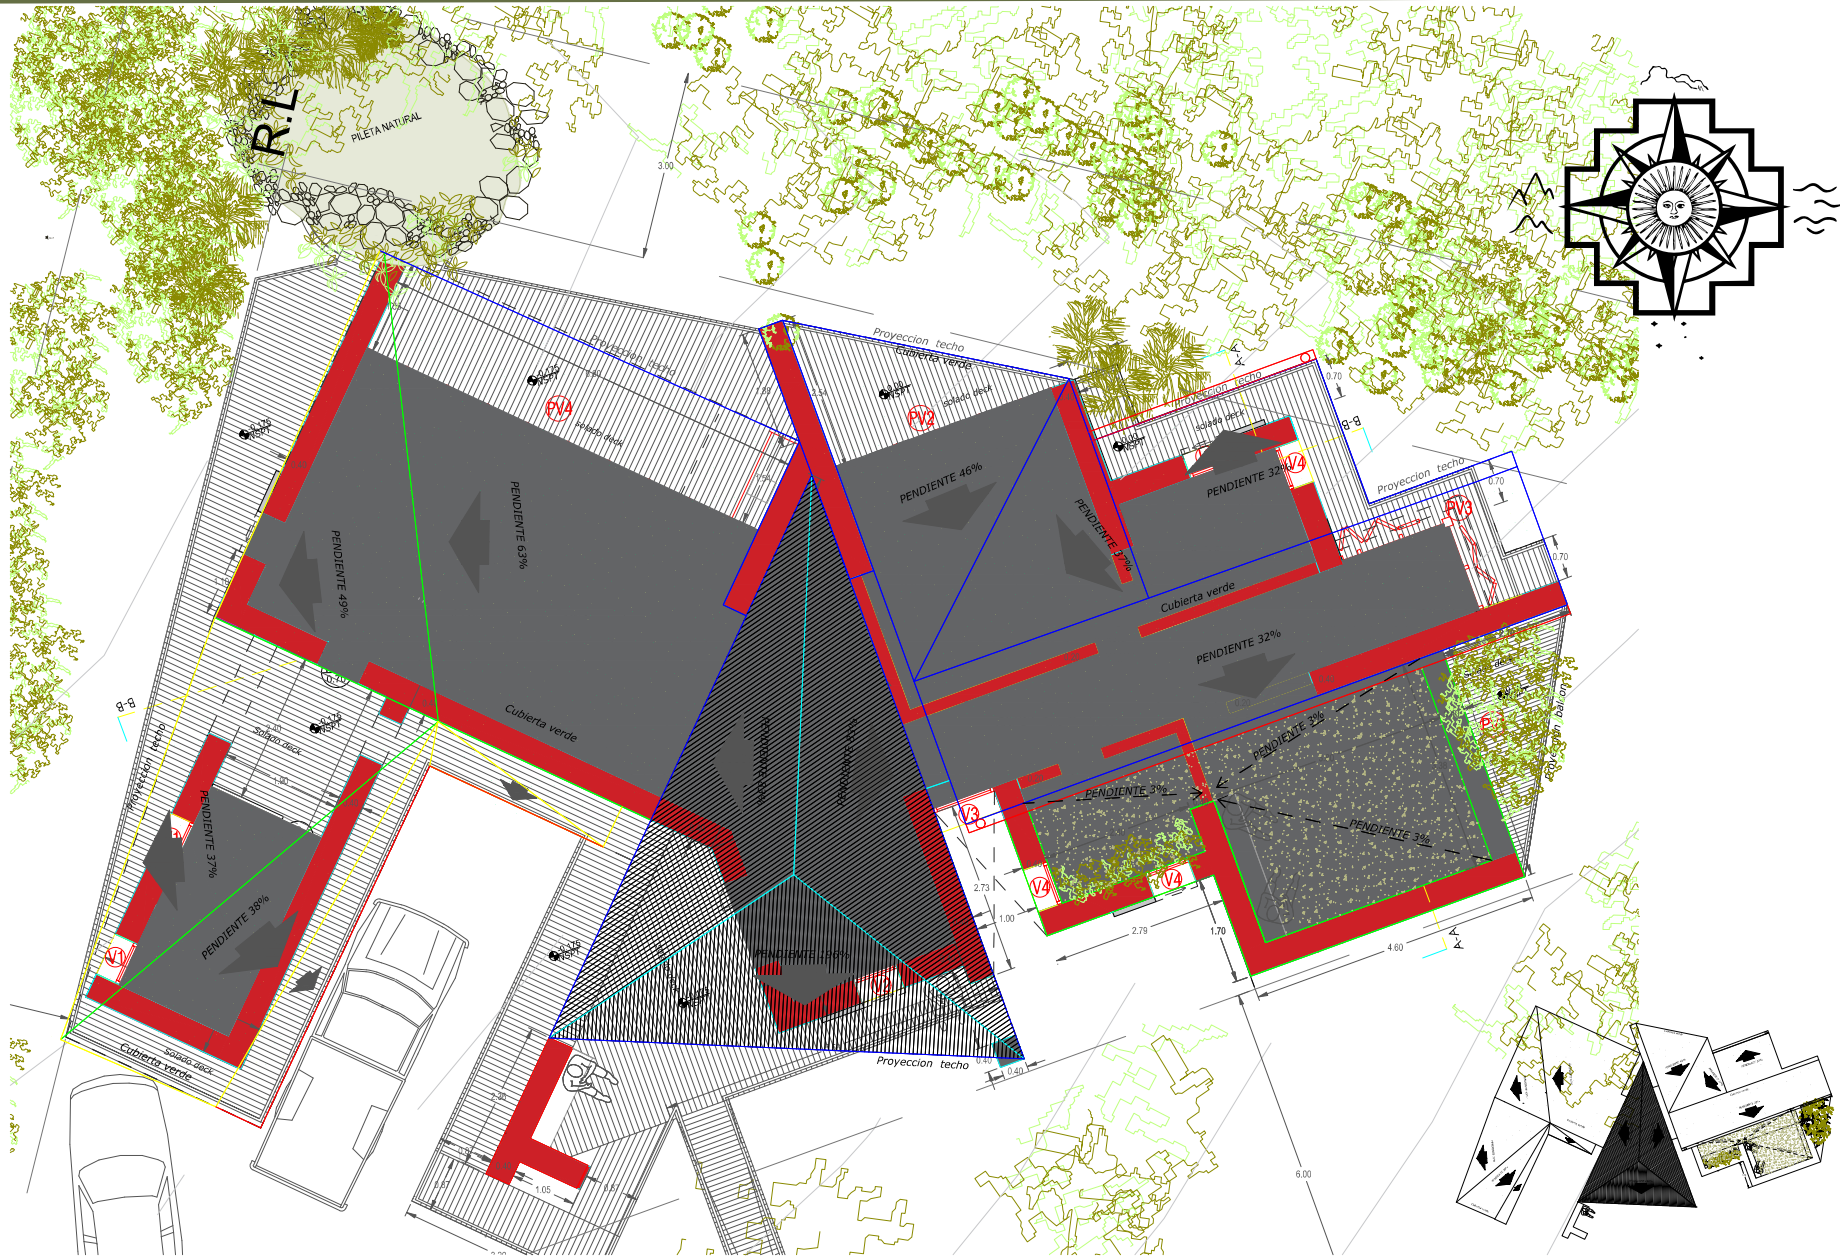


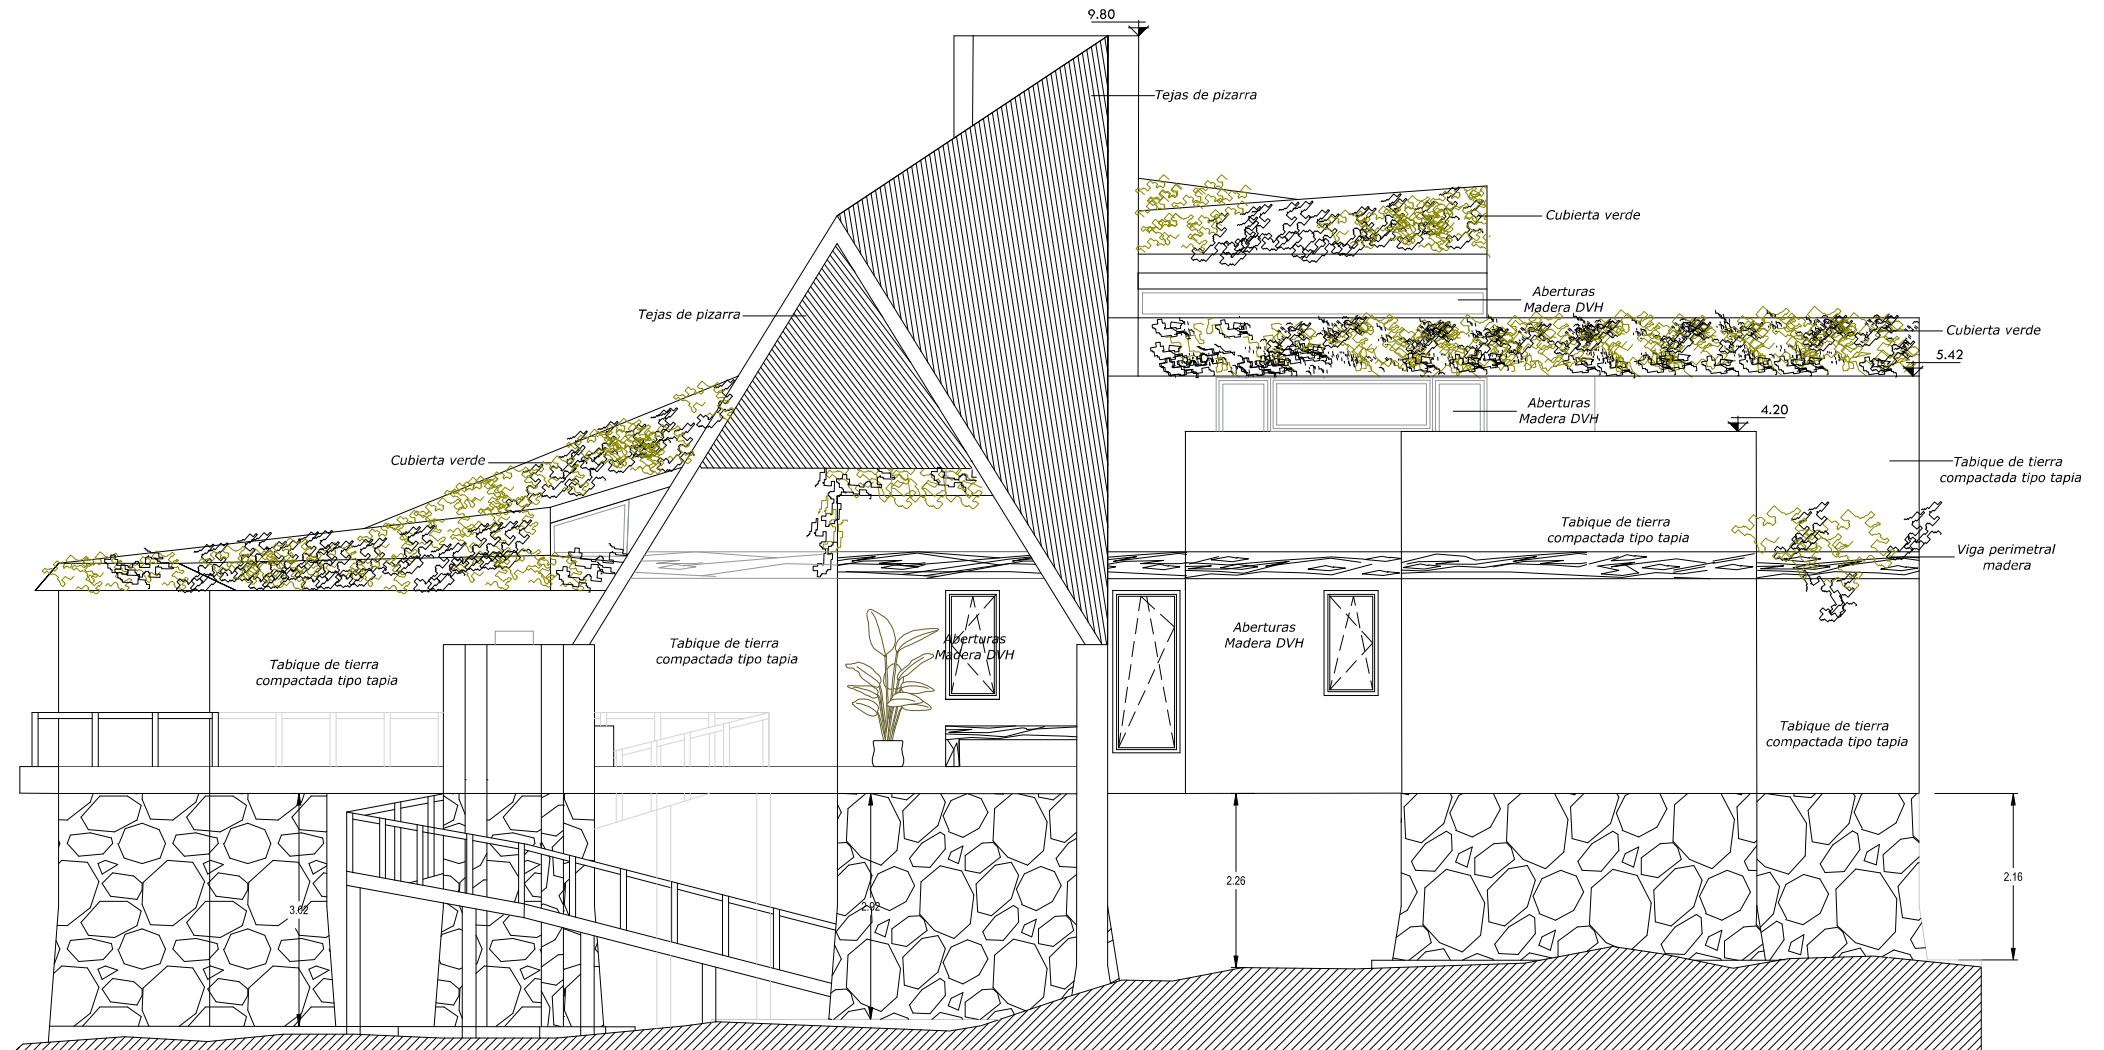


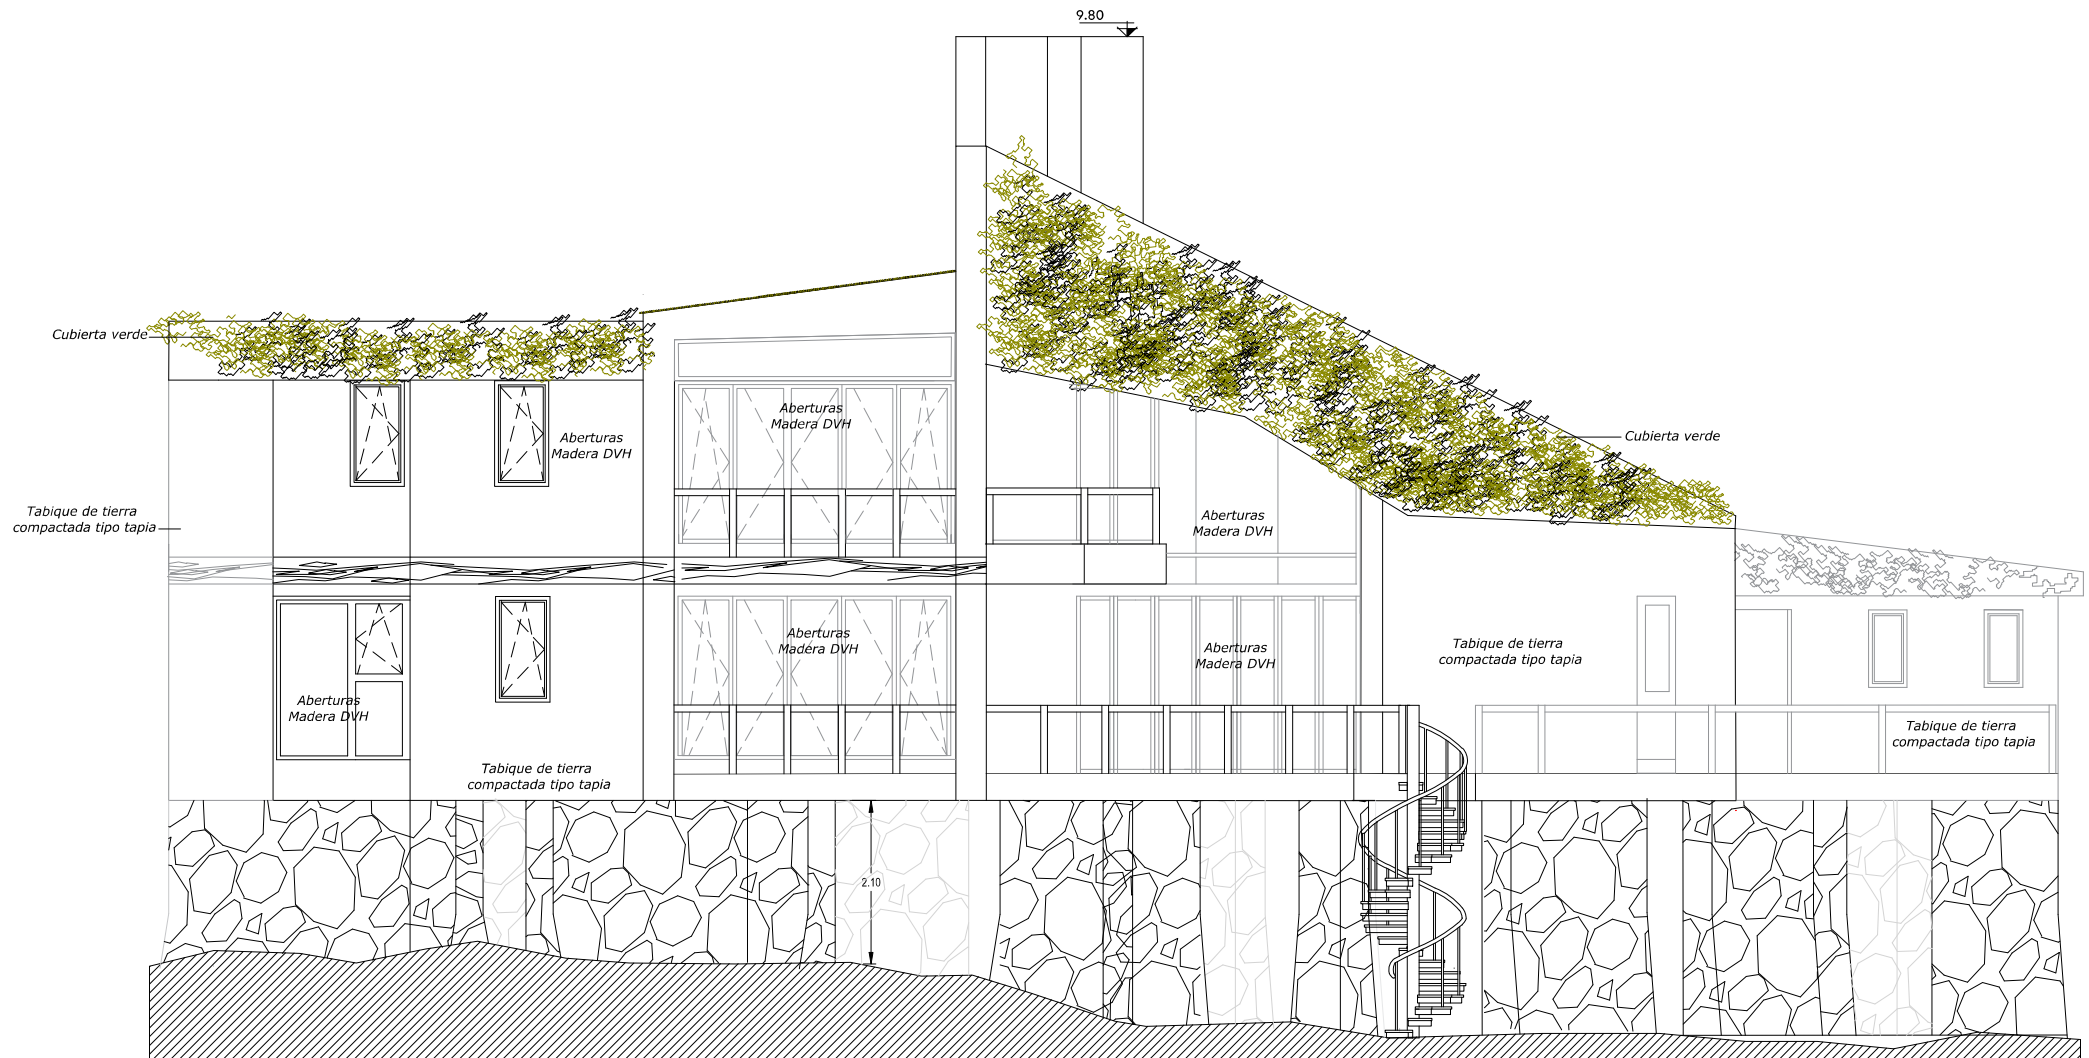


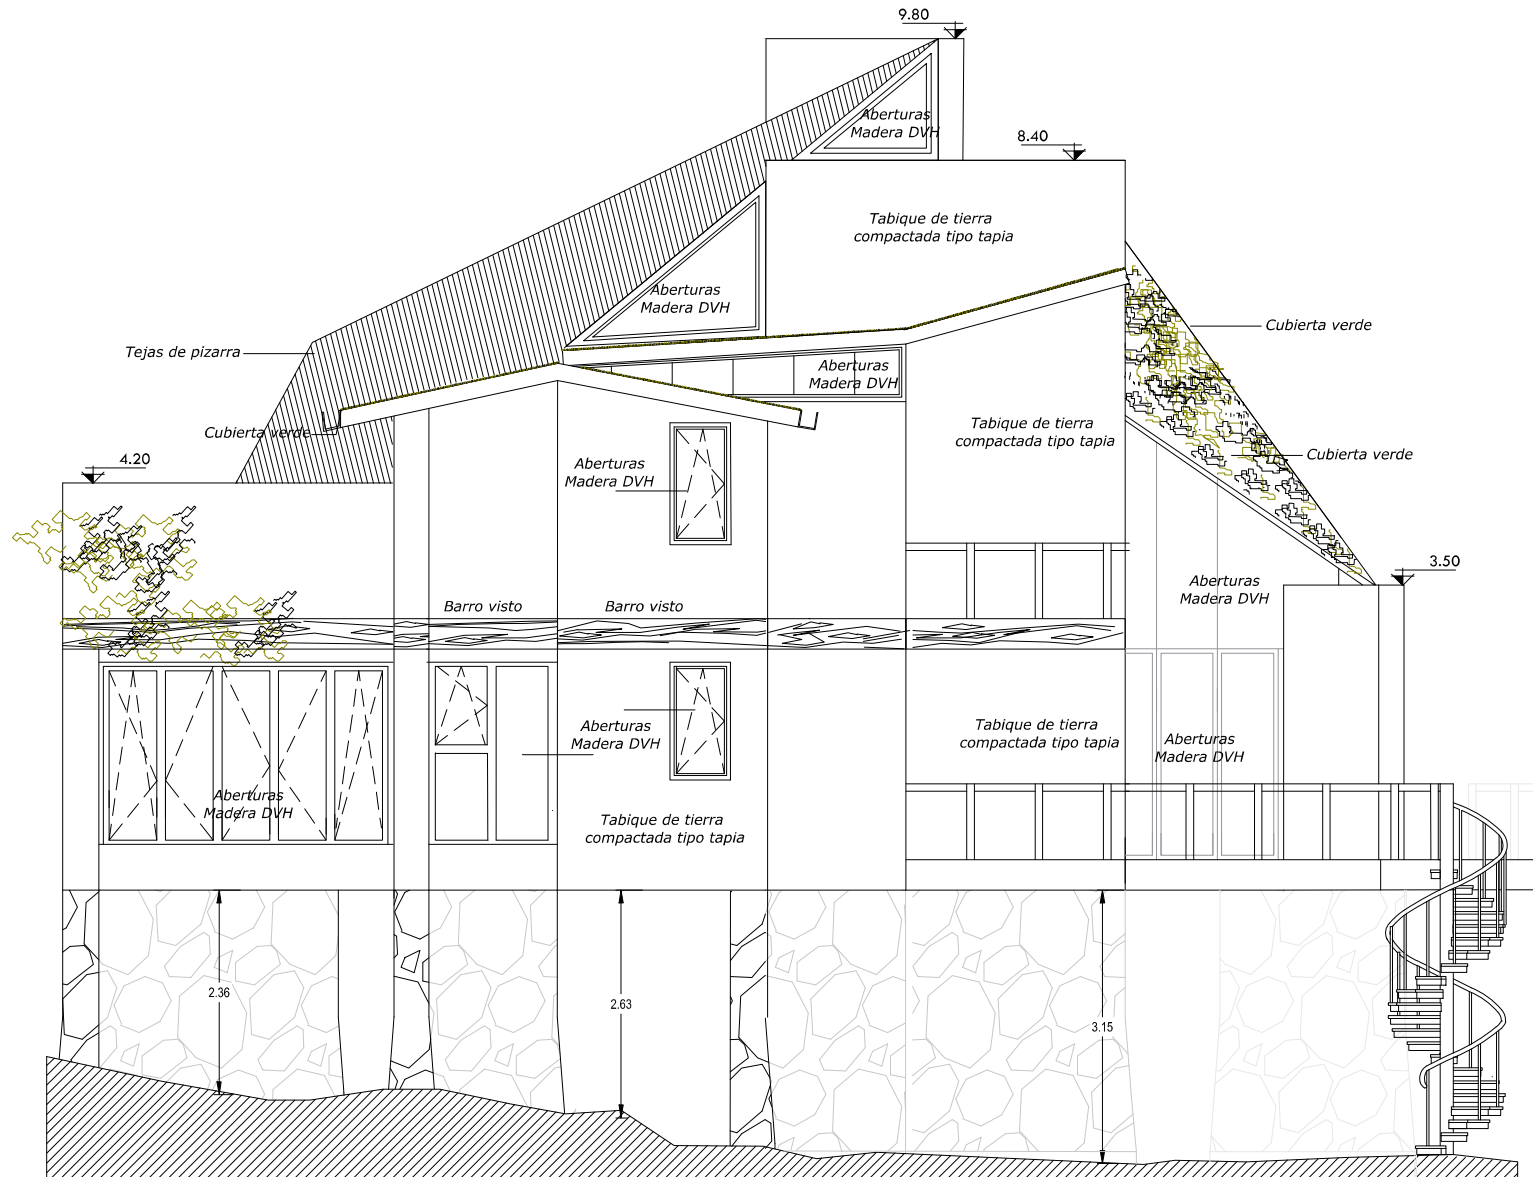

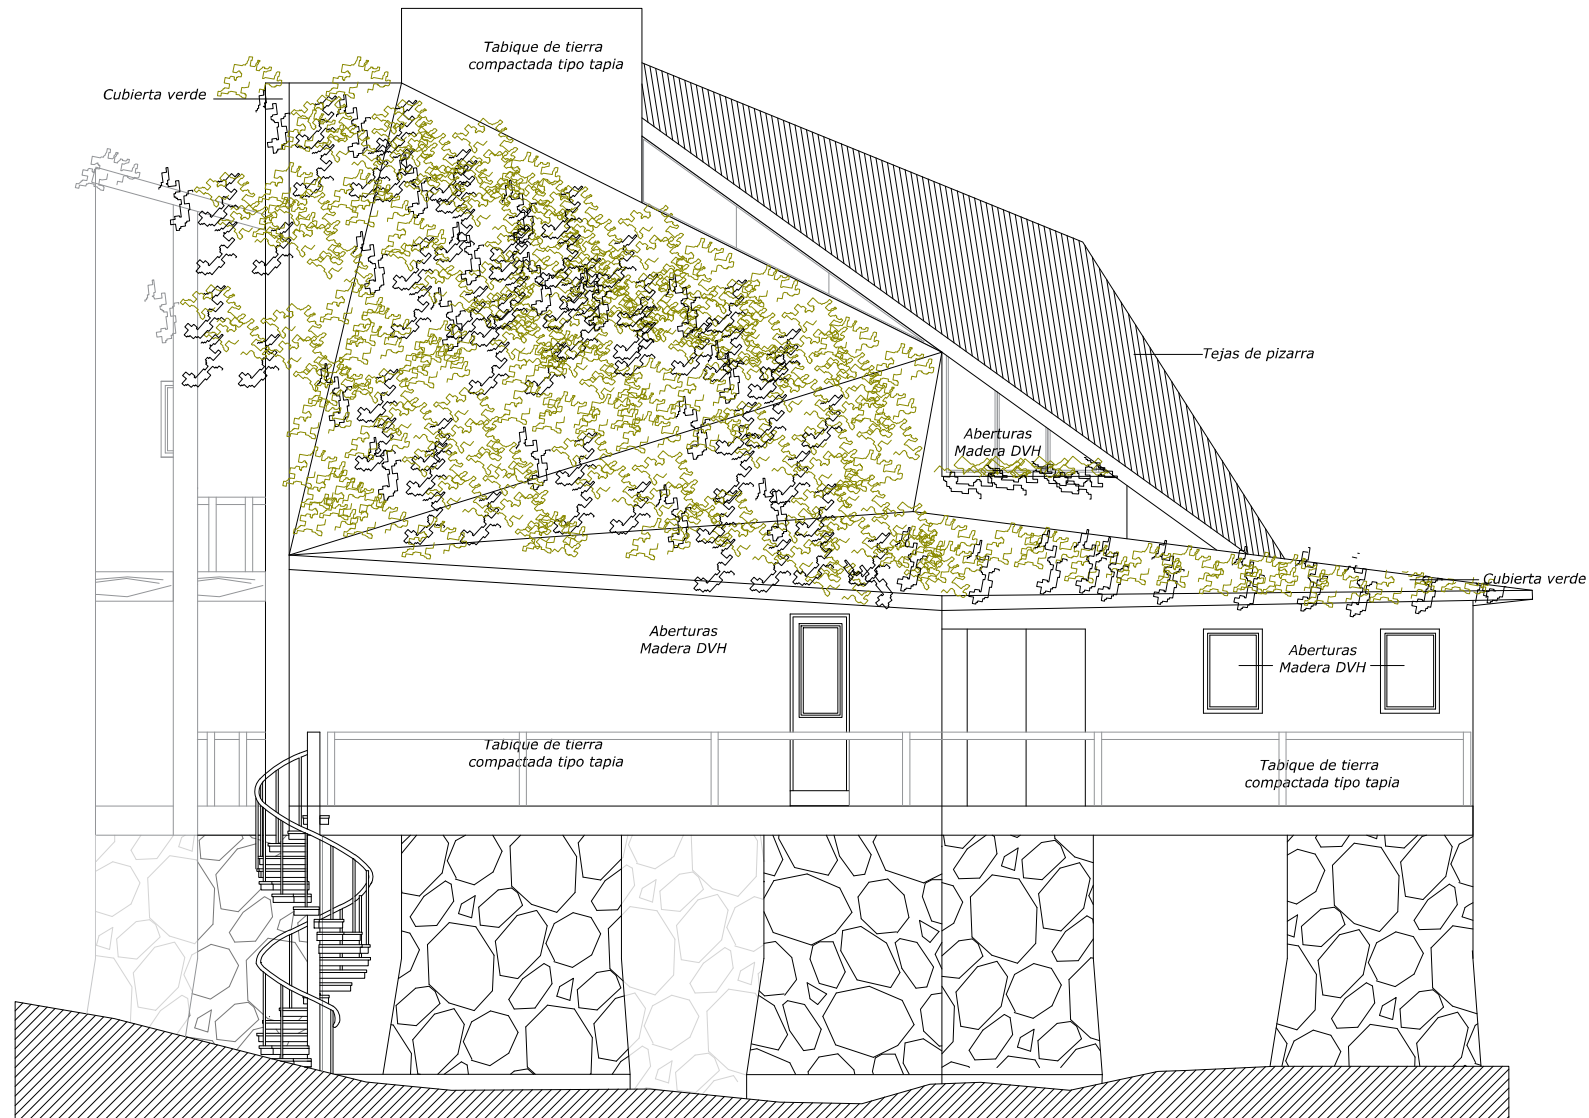


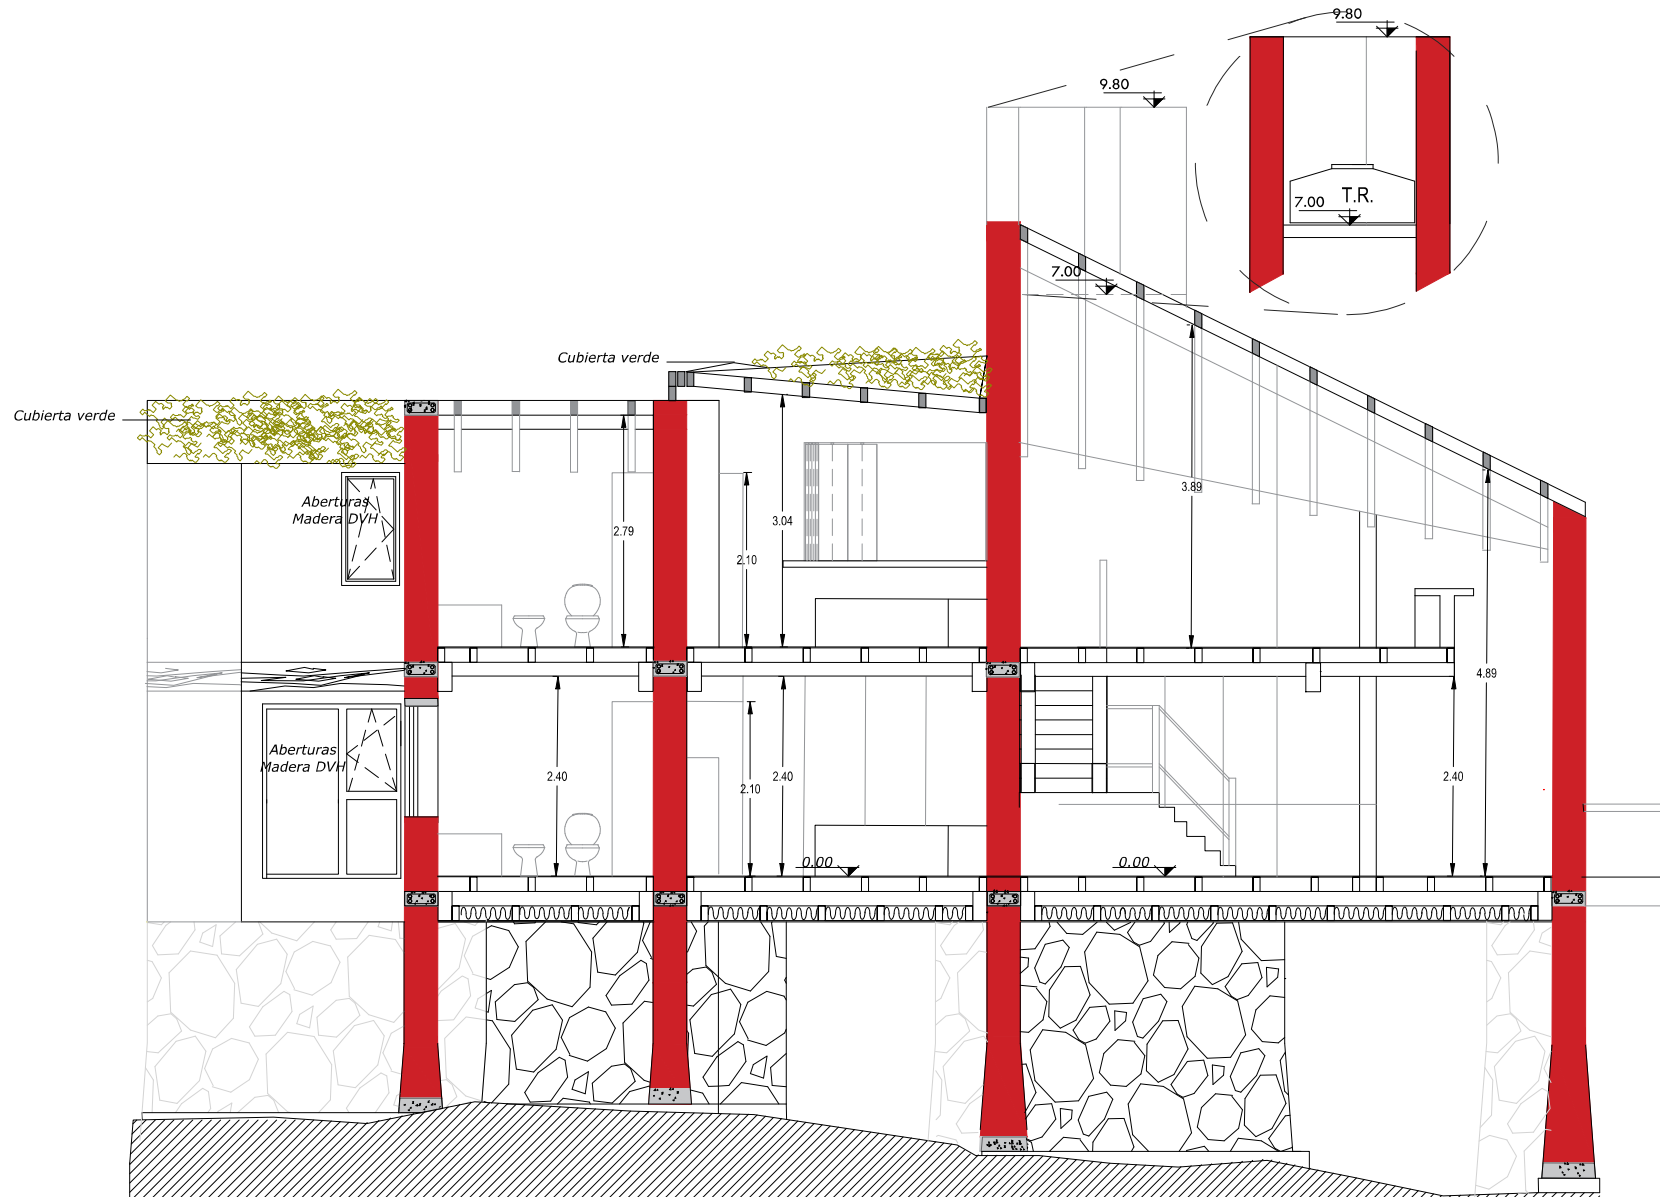

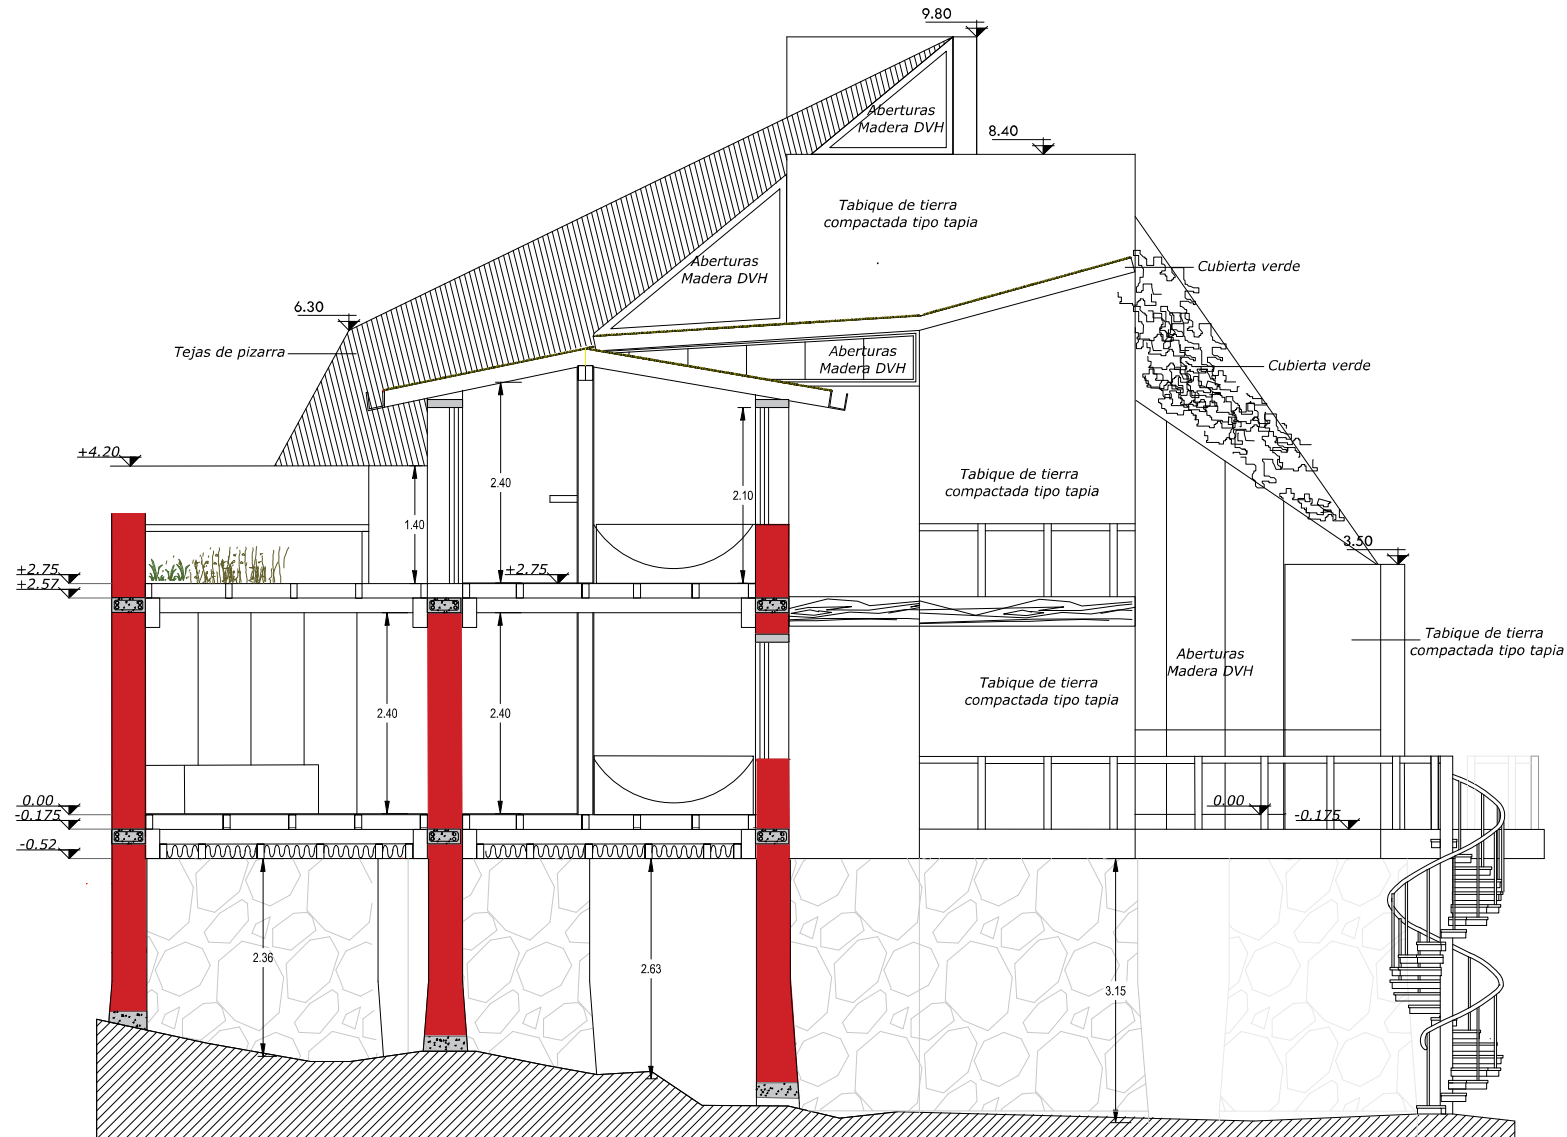


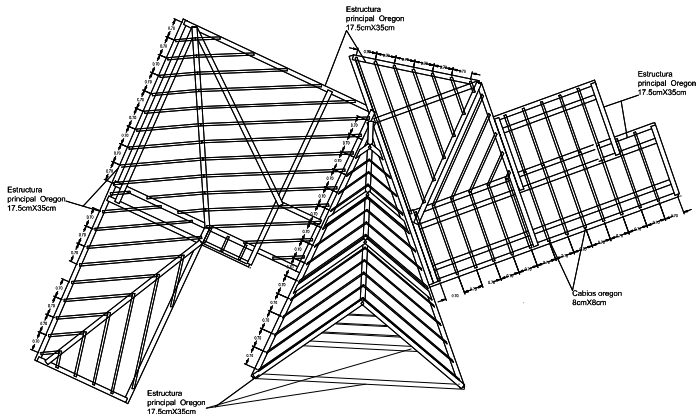


**PLANTA ESTRUCTURA DE
TECHOS 1:100**

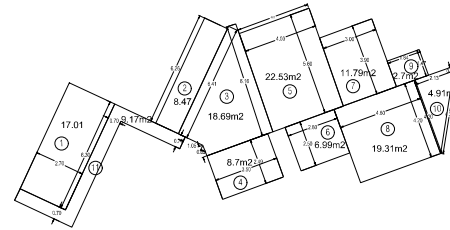


SILUETAS PB

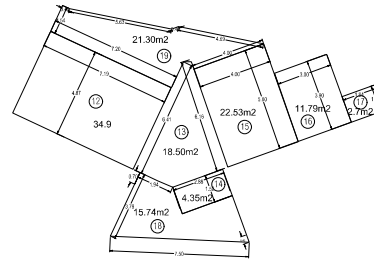



SILUETAS PA

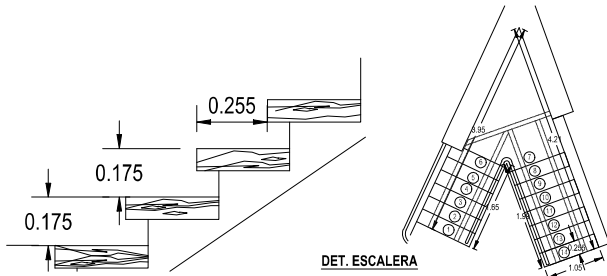

DET. ESCALERA

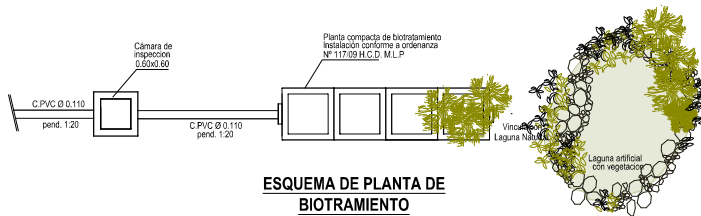

**ESQUEMA DE PLANTA DE
BIOTRAMIENTO**

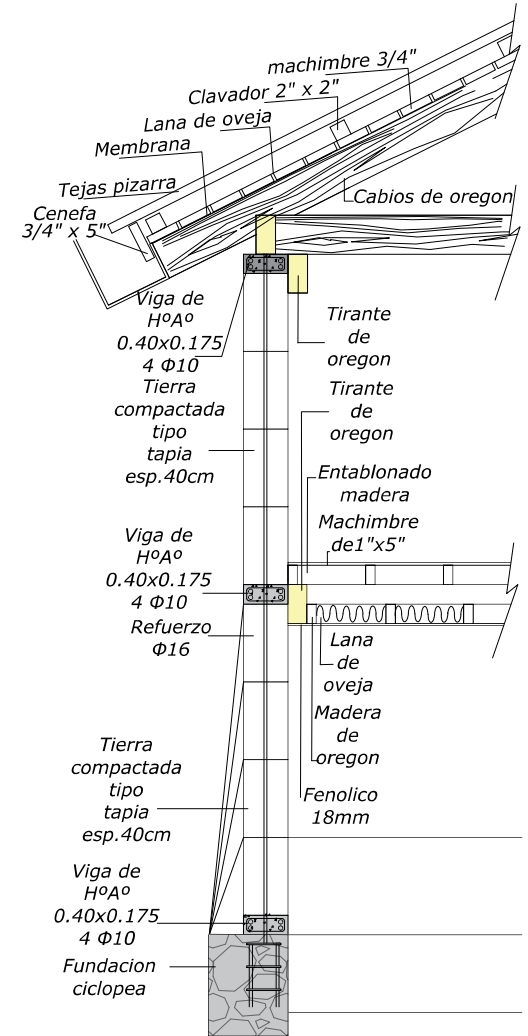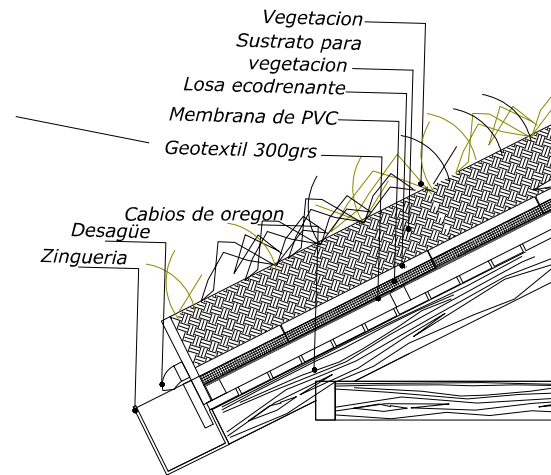

CORTE CONSTRUCTIVO 1:25



