




PROYECTO MAHUIDA




EL BOLSÓN - LAGO PUELO / COMARCA ANDINA - PATAGONIA - ARGENTINA



el sol de frente
ciclo de luz y sombras
sobre mahuida


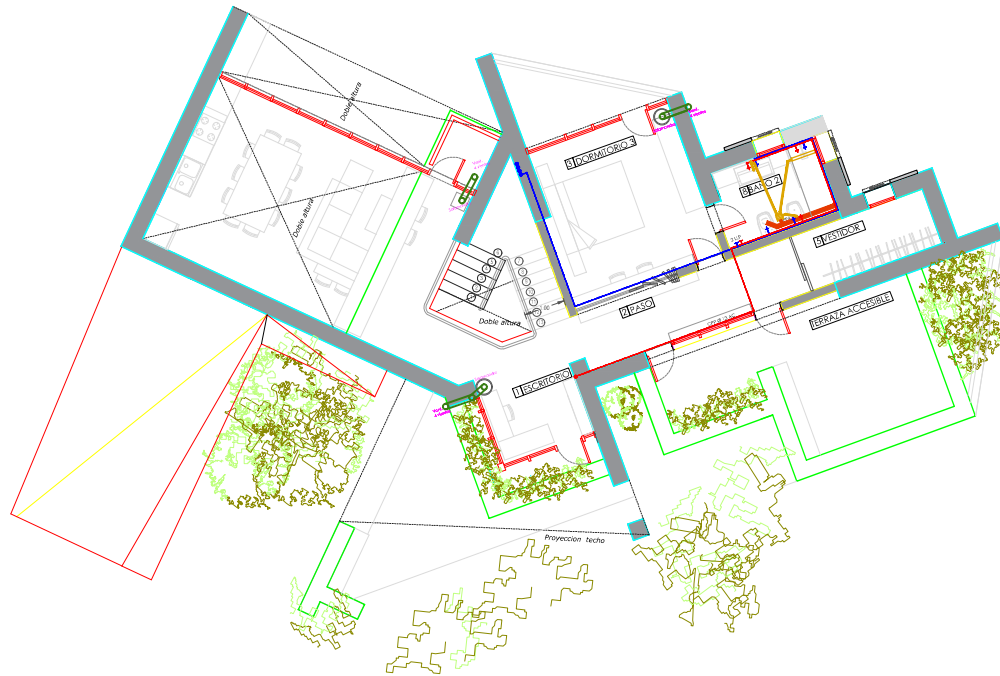



TANQUE DE RESERVA
tanque reserva cap. 1000lt.
alimentac. mang. polip. Ø13mm.
1 llaves de paso Ø 19mm.
3 llaves de paso Ø 13mm.
desb. y limp. Ø 25mm.
c.v. cpvc Ø25mm.

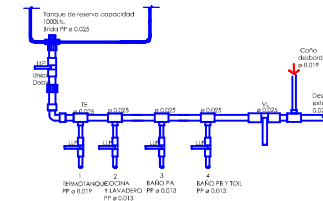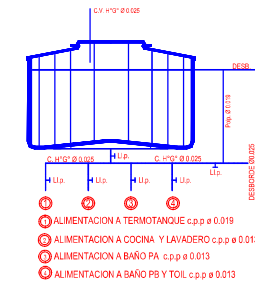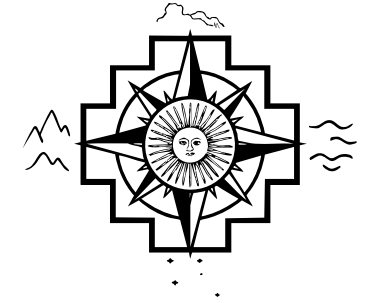



LA INSTALACION SANITARIA CUMPLE EN SU TOTALIDAD CON LA ORDENANZA N° 117/09 MLP.

NO SE UBICARAN ELEMENTOS DE LA INSTALACION SANITARIA A UNA DISTANCIA MENOR DE 2.50 m DE LOS LIMITES DEL TERRENO.

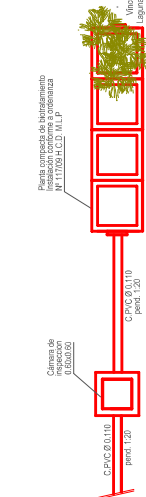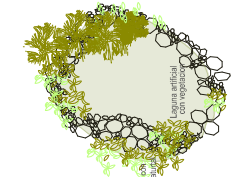

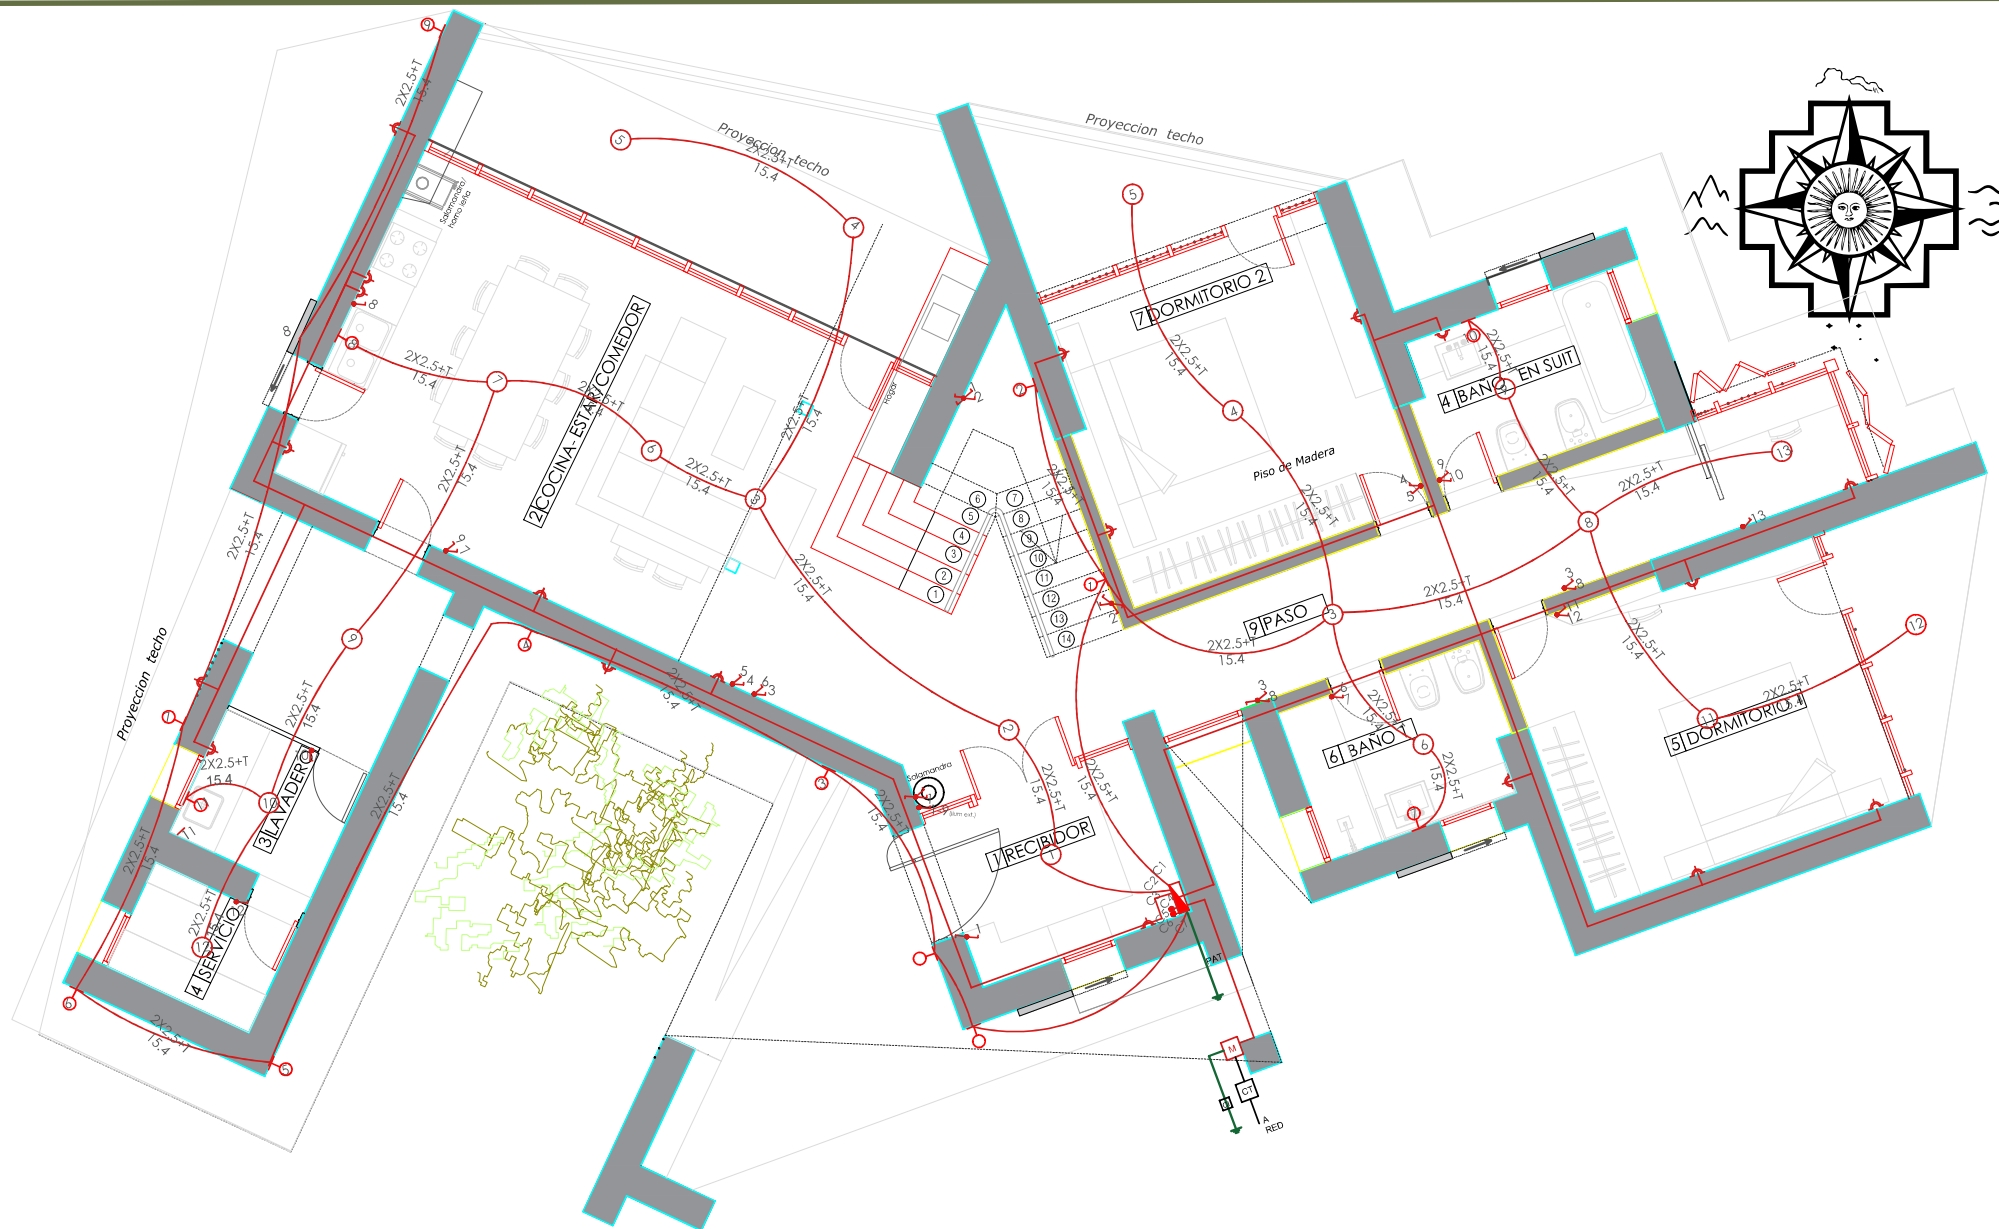

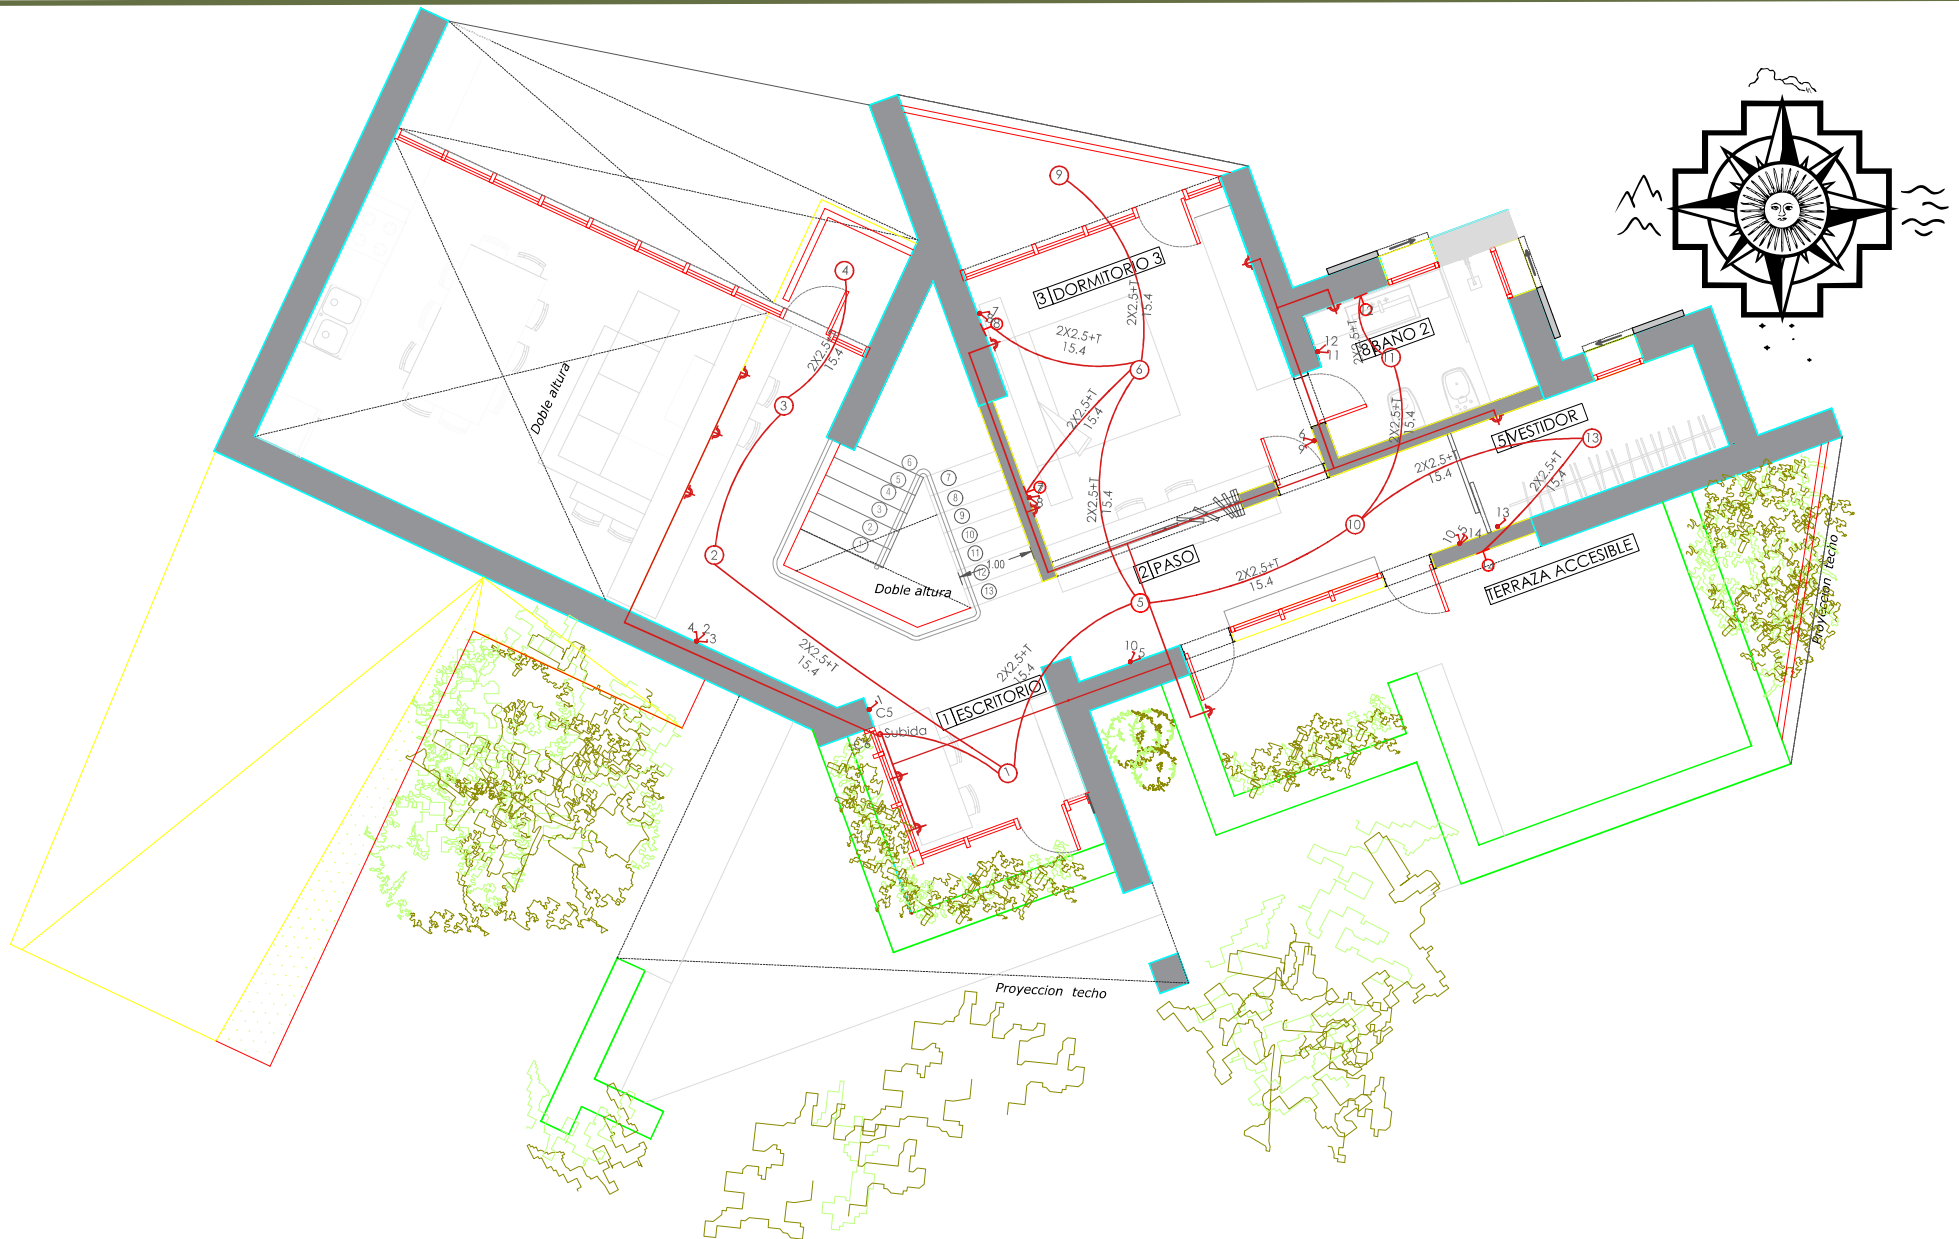


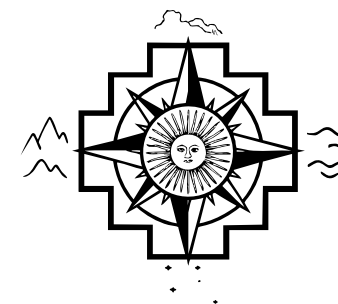


E.M1
E.M2



ETIRO LATERAL



RETIRO FRENTE



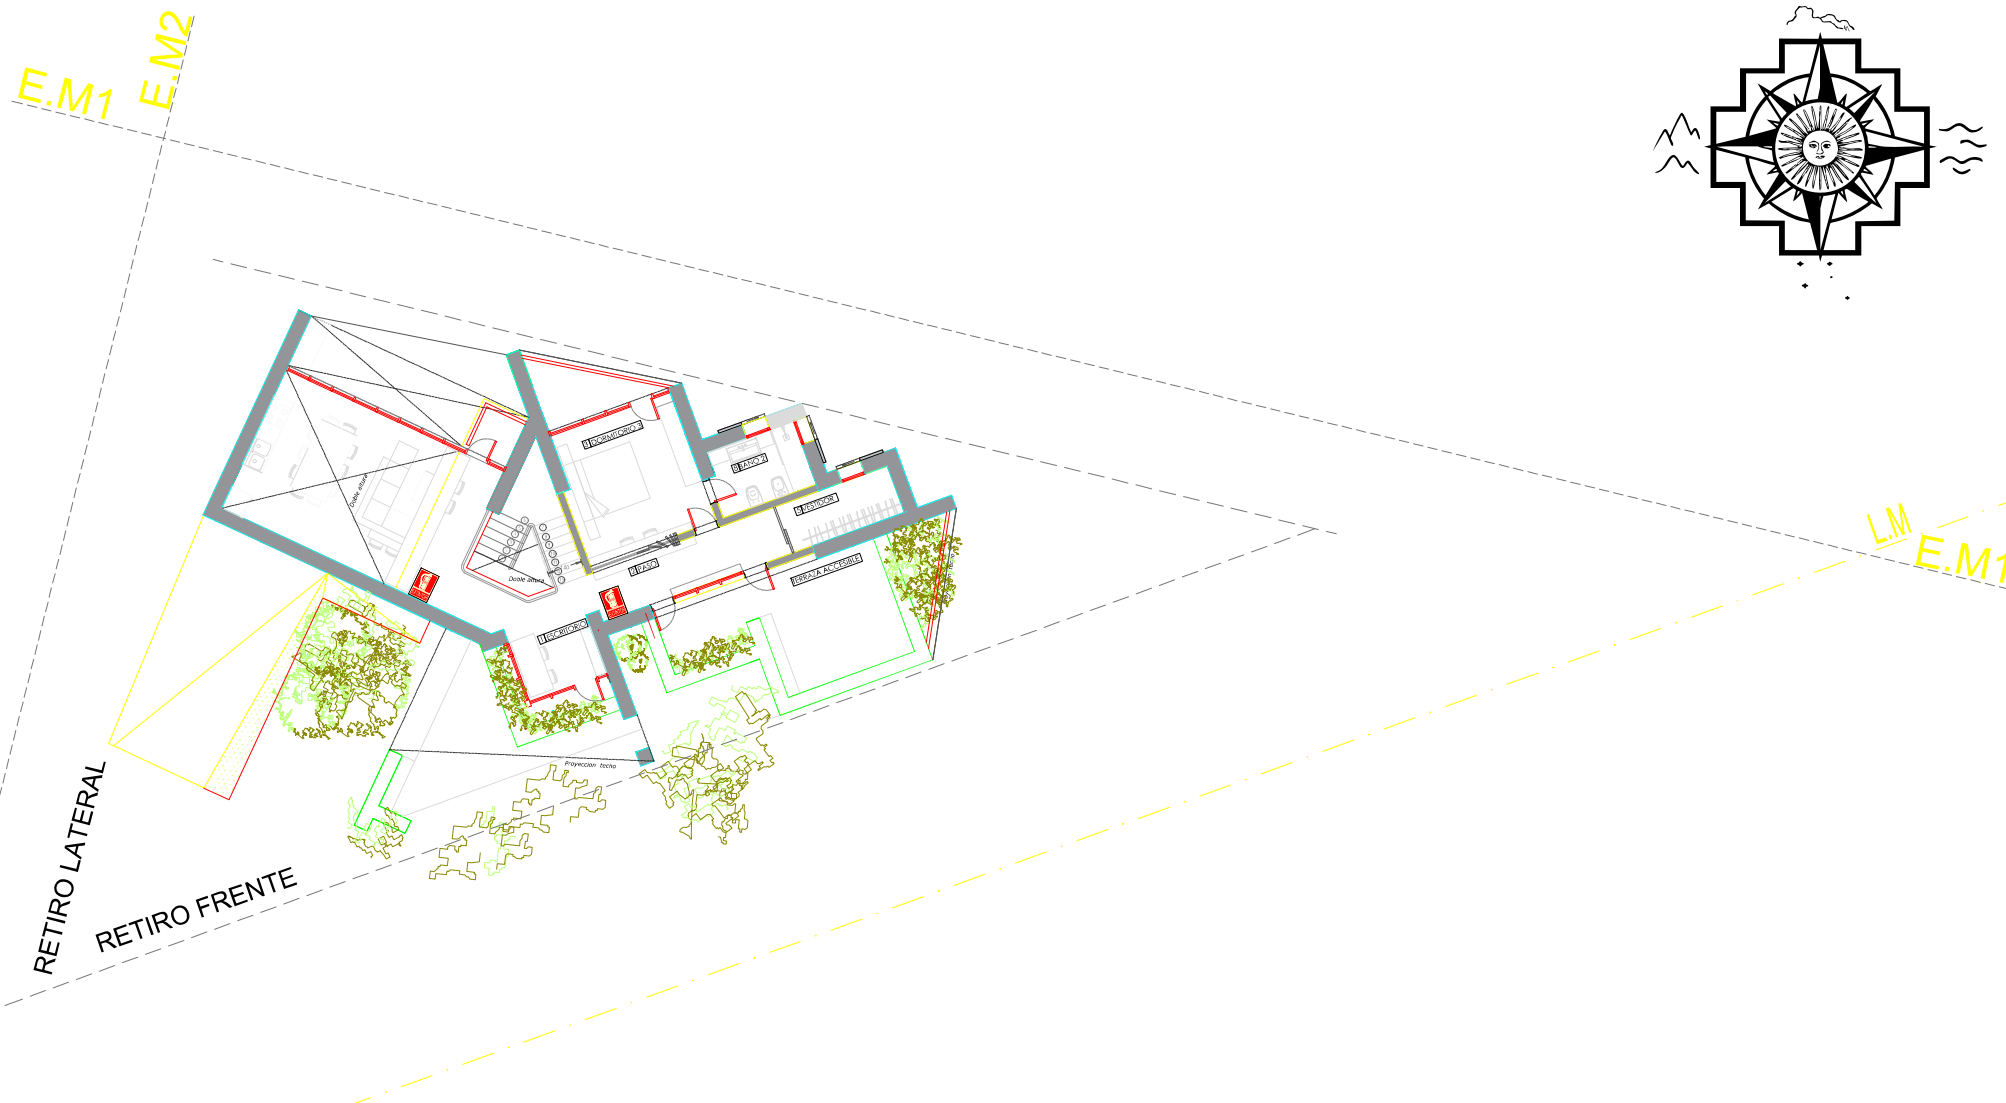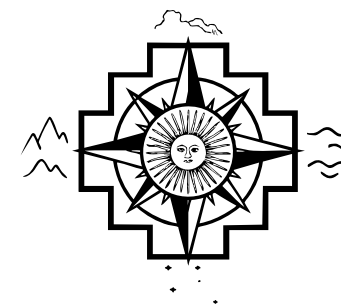


SE CONTEMPLA EL SISTEMA DE RIEGO PERIMETRAL Y SUPERFICIAL DEL TERRENO Y EL TECHO VERDE COMO COMPLEMENTO PARA PREVENCIÓN Y EVACUACIÓN. LOS TANQUES DE INUNDACIÓN QUE SE PROYECTAN EN EL LADO MAS ALTO DEL TERRENO DEBERÁN ADMITIR USO PARA ALIMENTAR MOTOBOMBAS

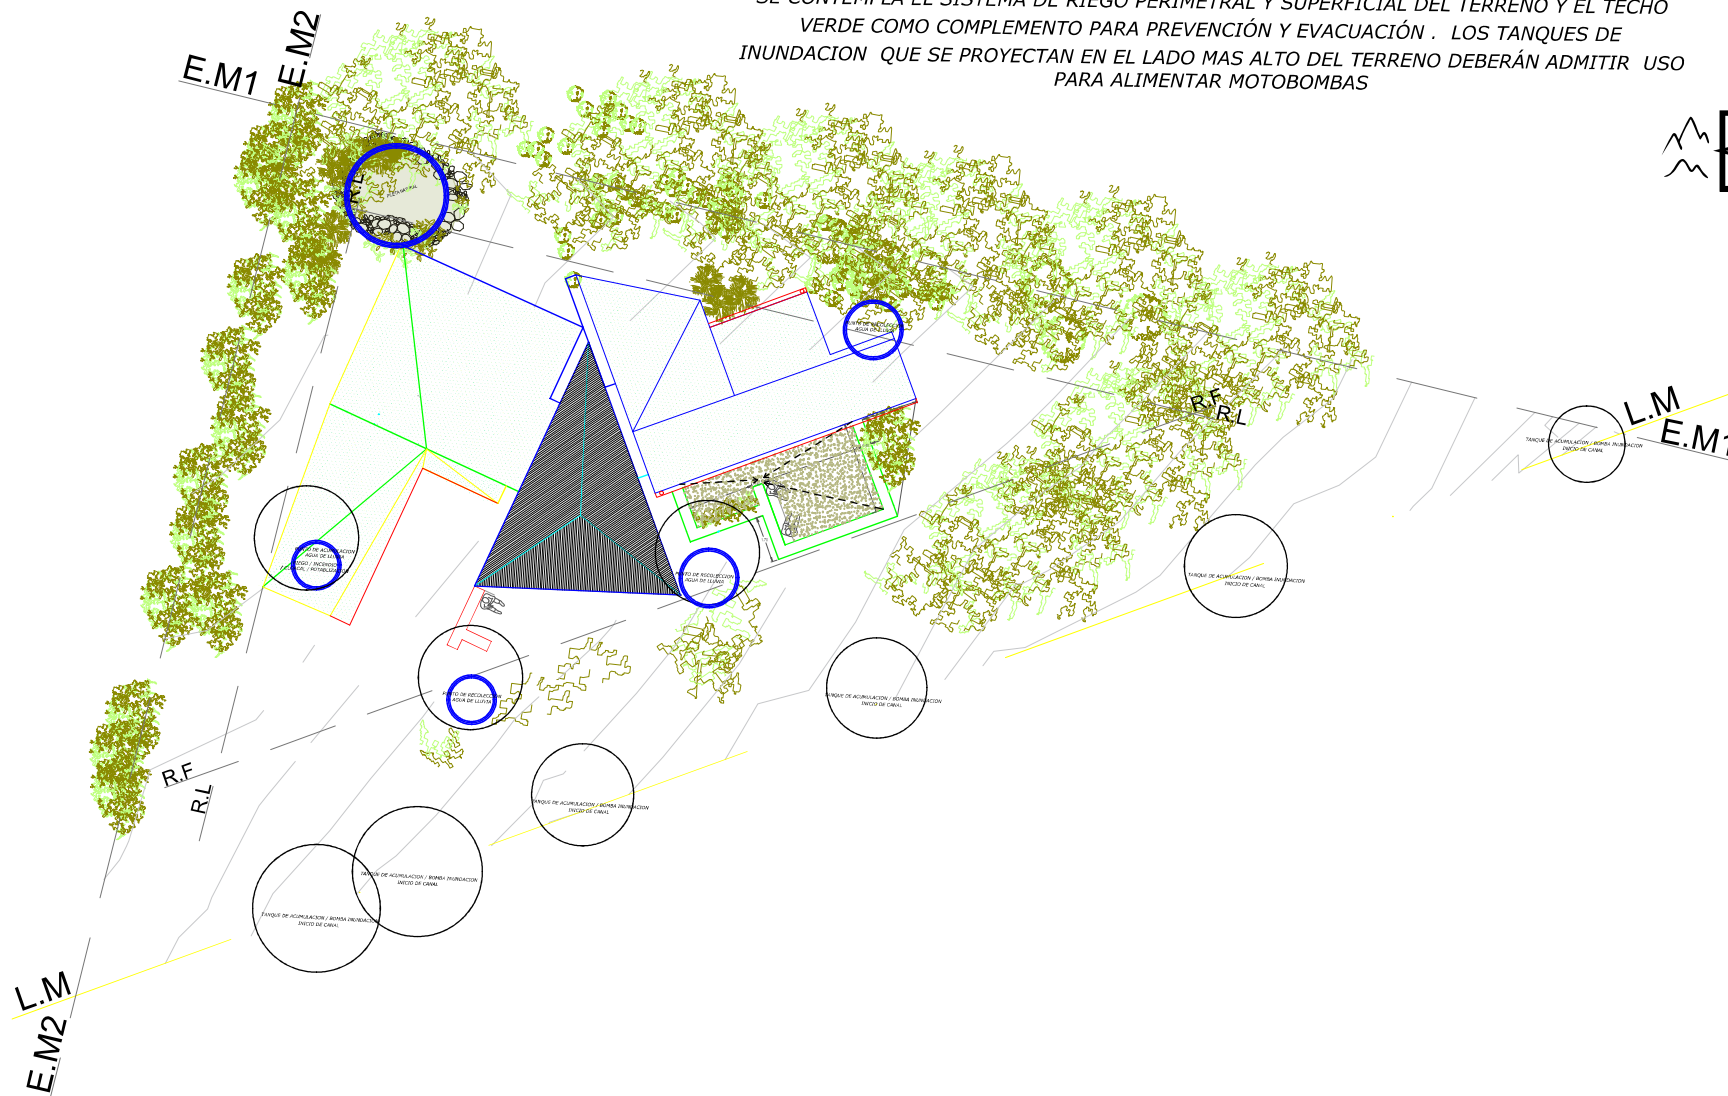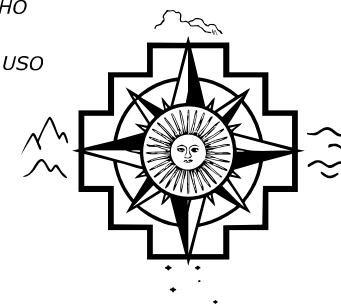


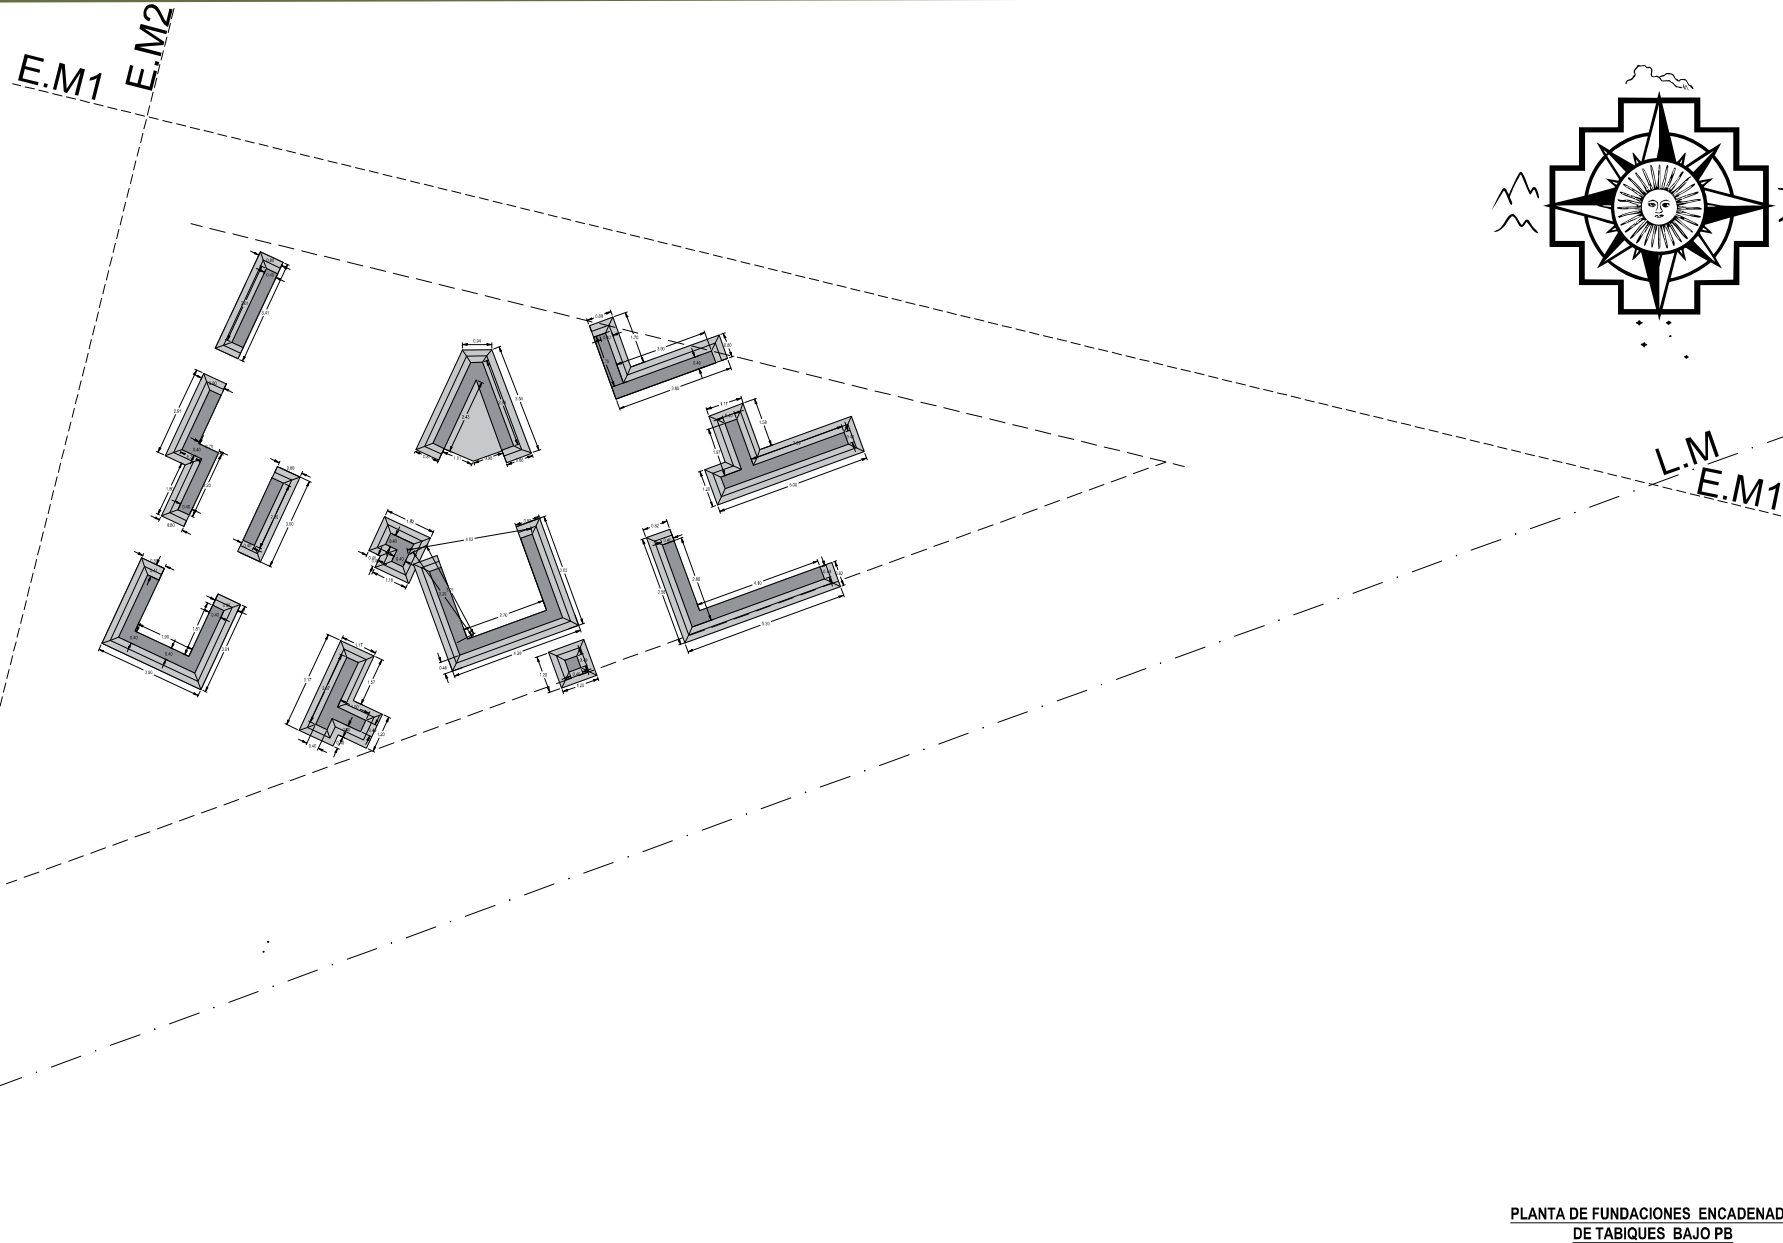
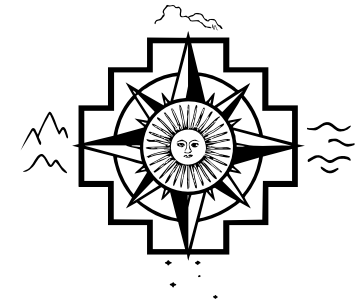



PLANTA DE FUNDACIONES ENCADENADO
DE TABIQUES BAJO PB

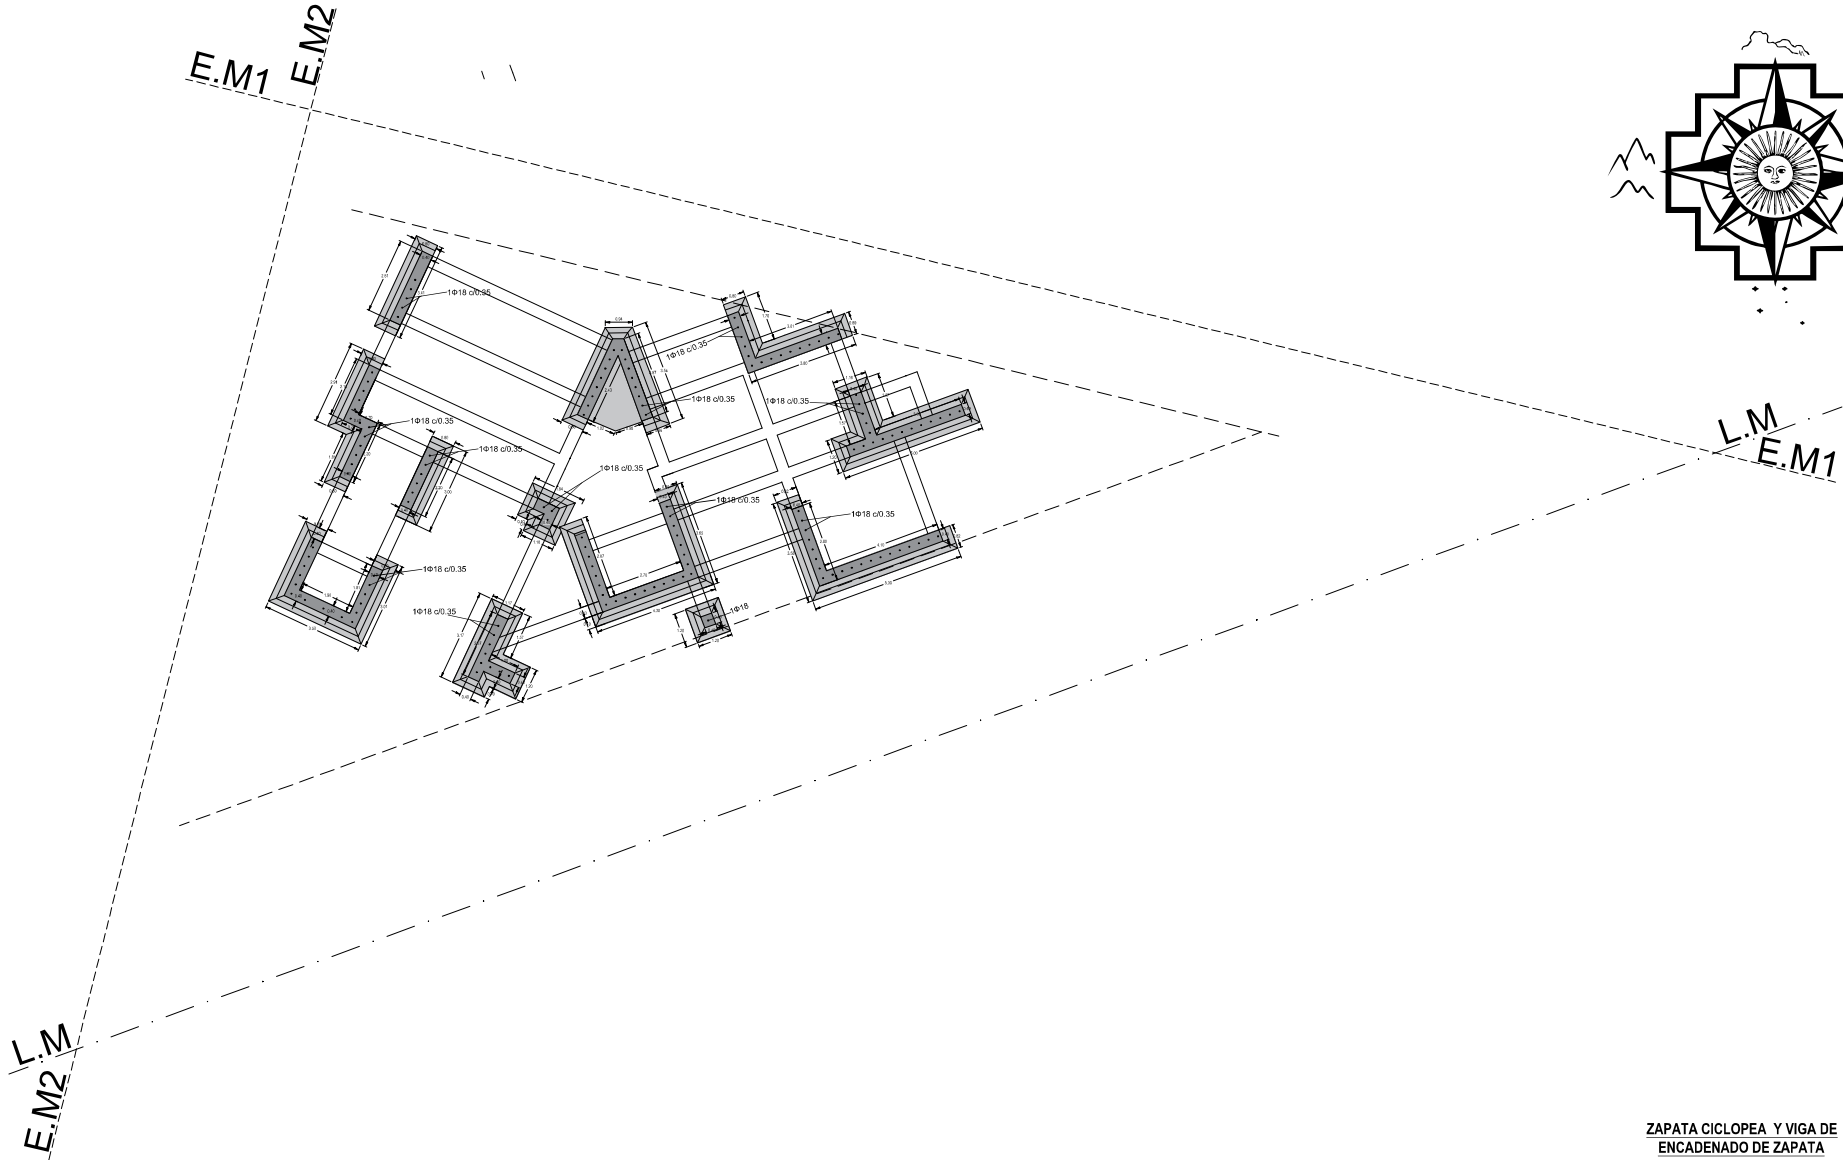


ZAPATA CICLOPEA Y VIGA DE
ENCADENADO DE ZAPATA

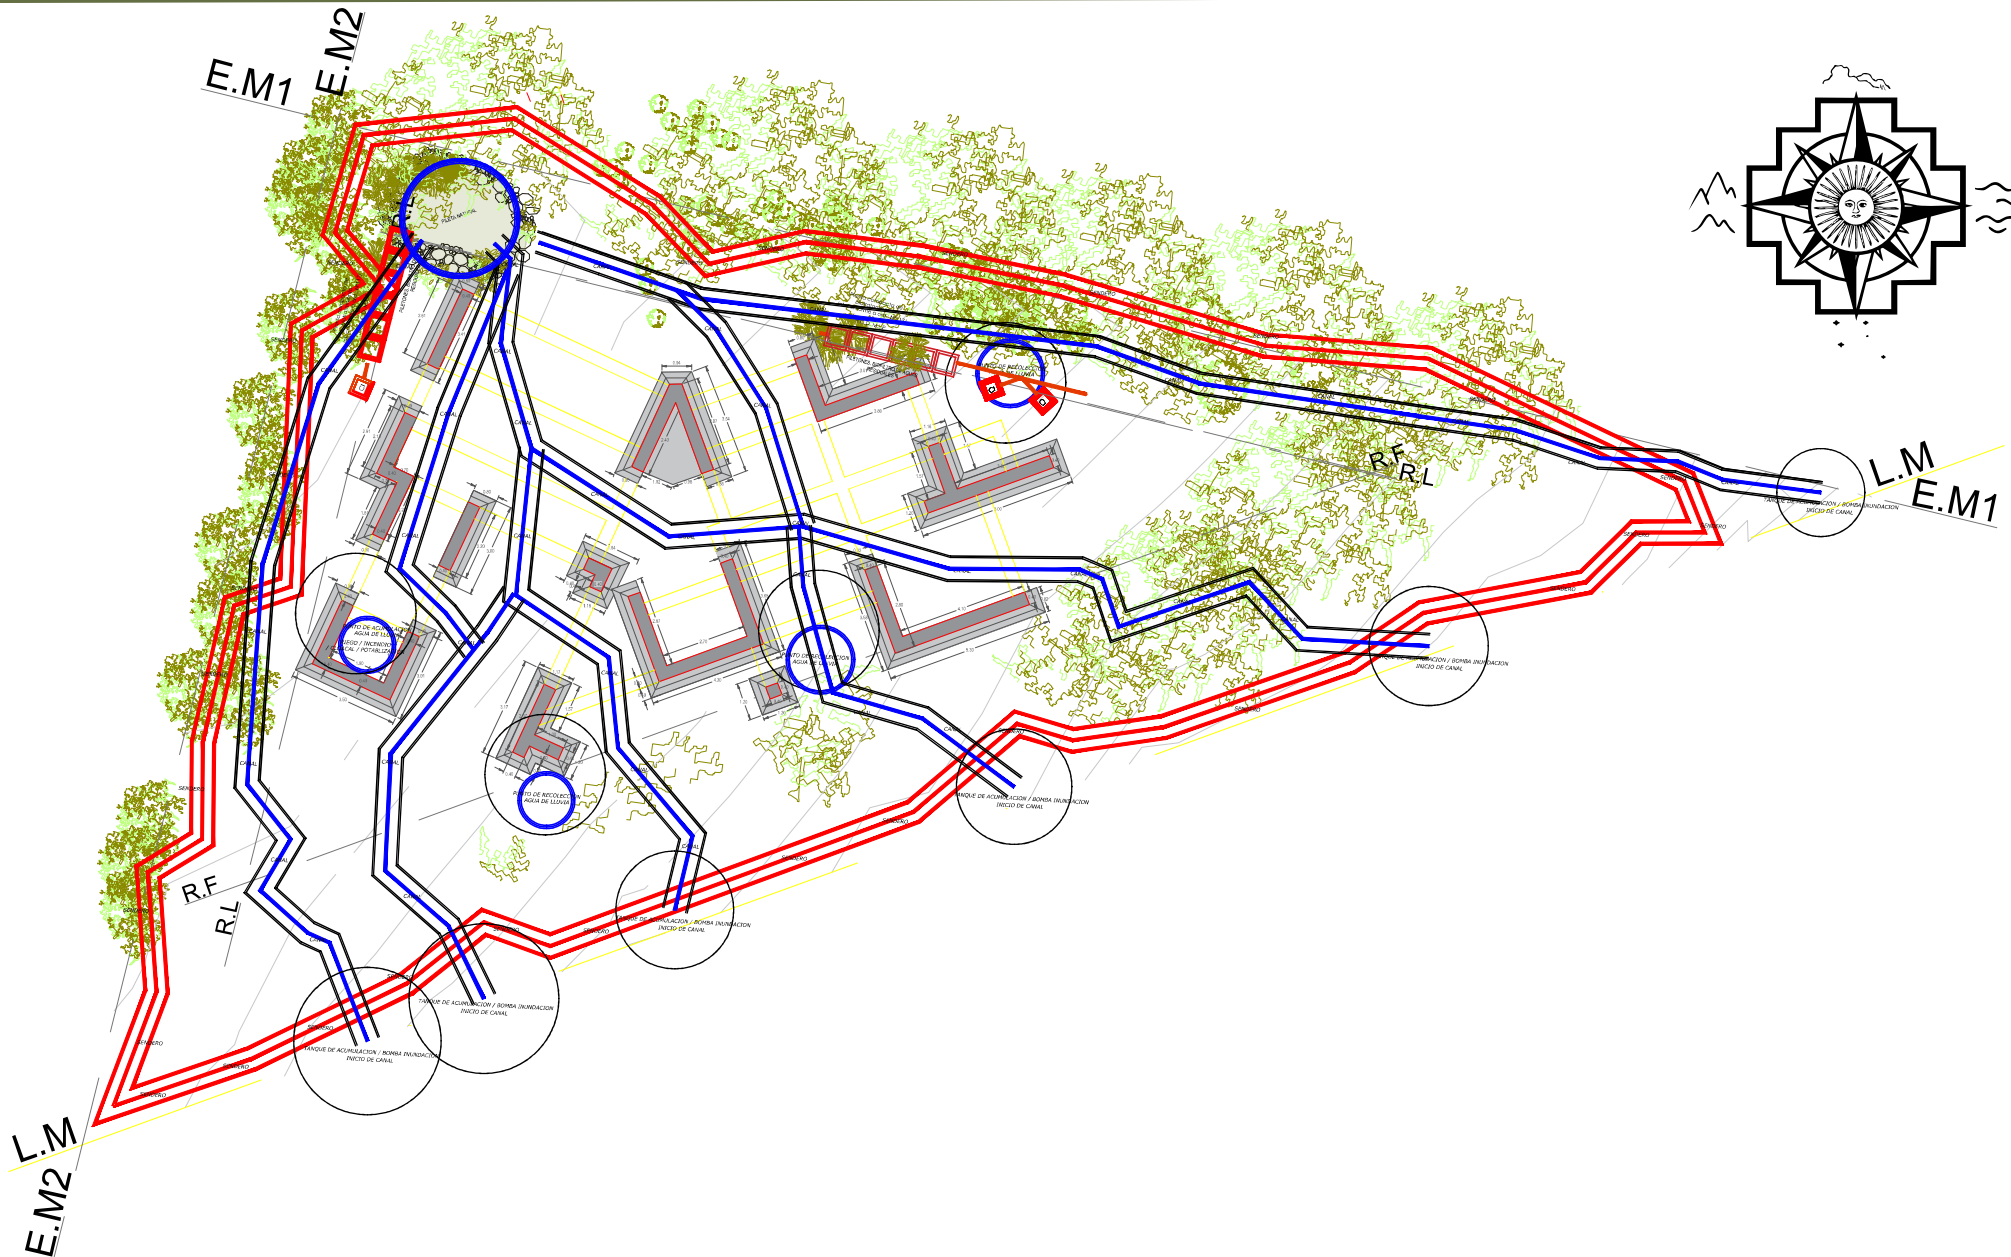


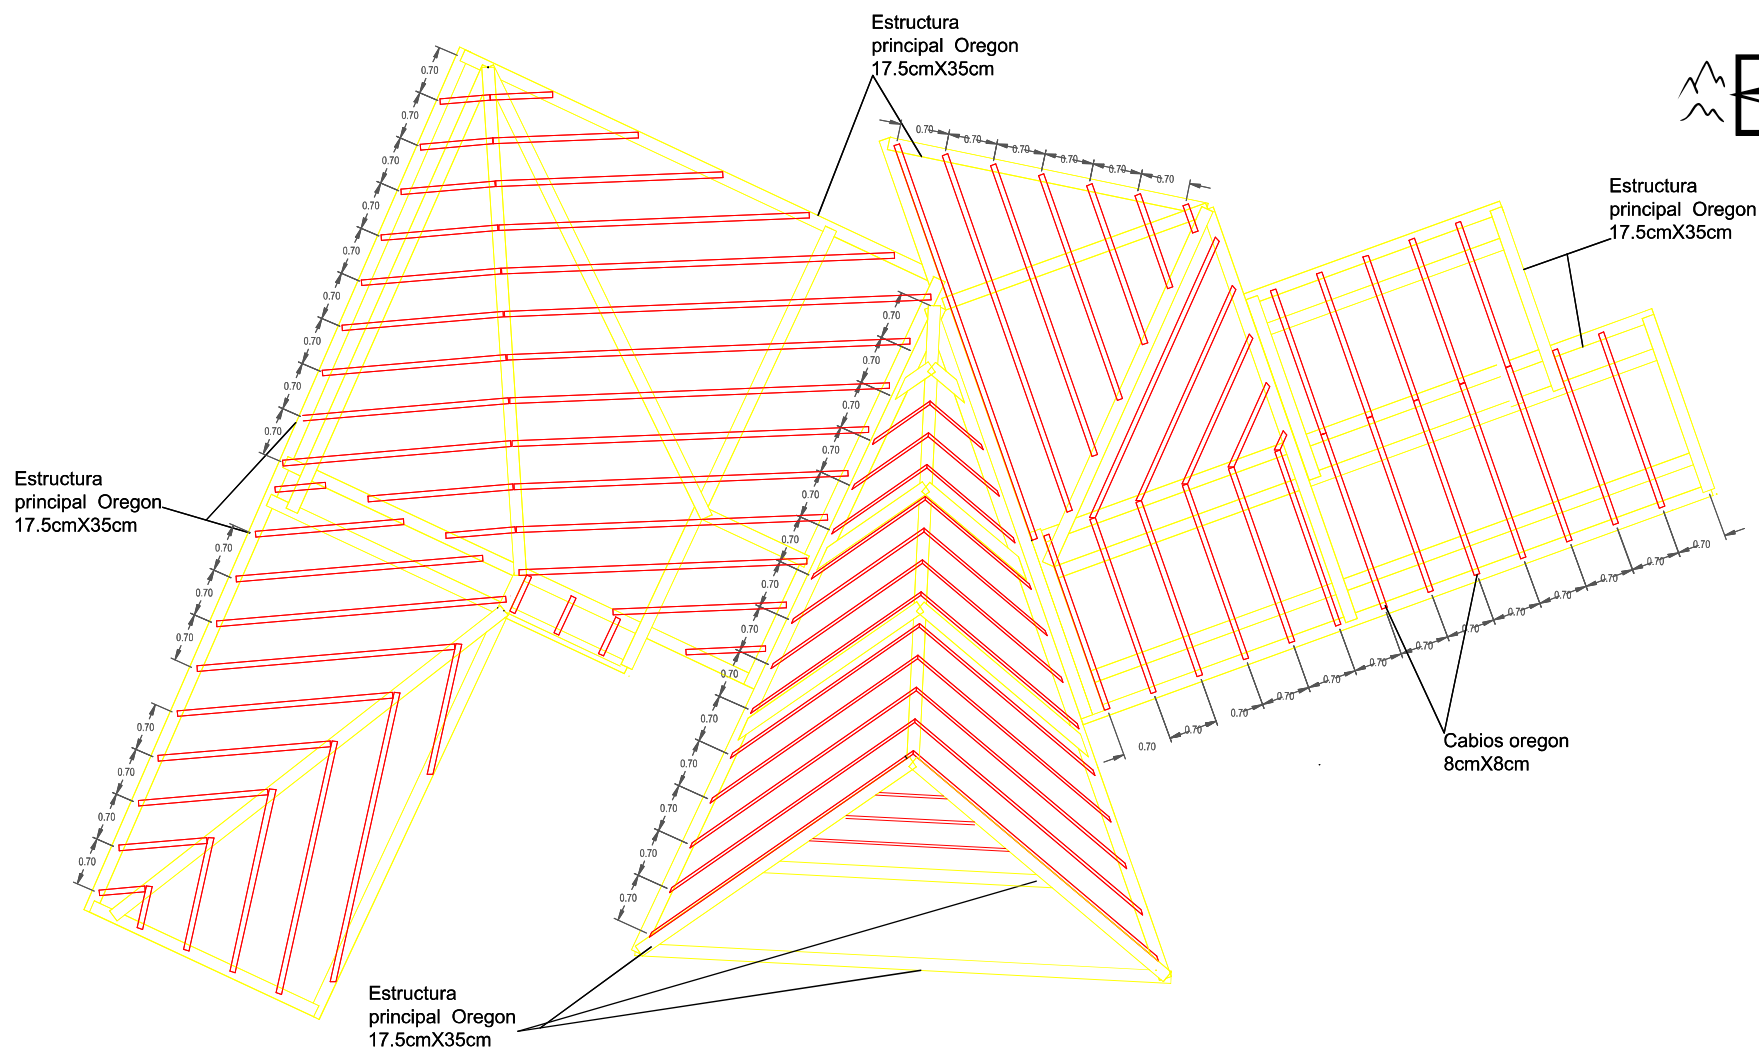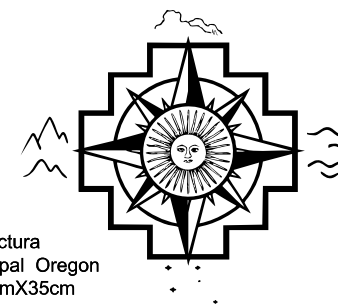


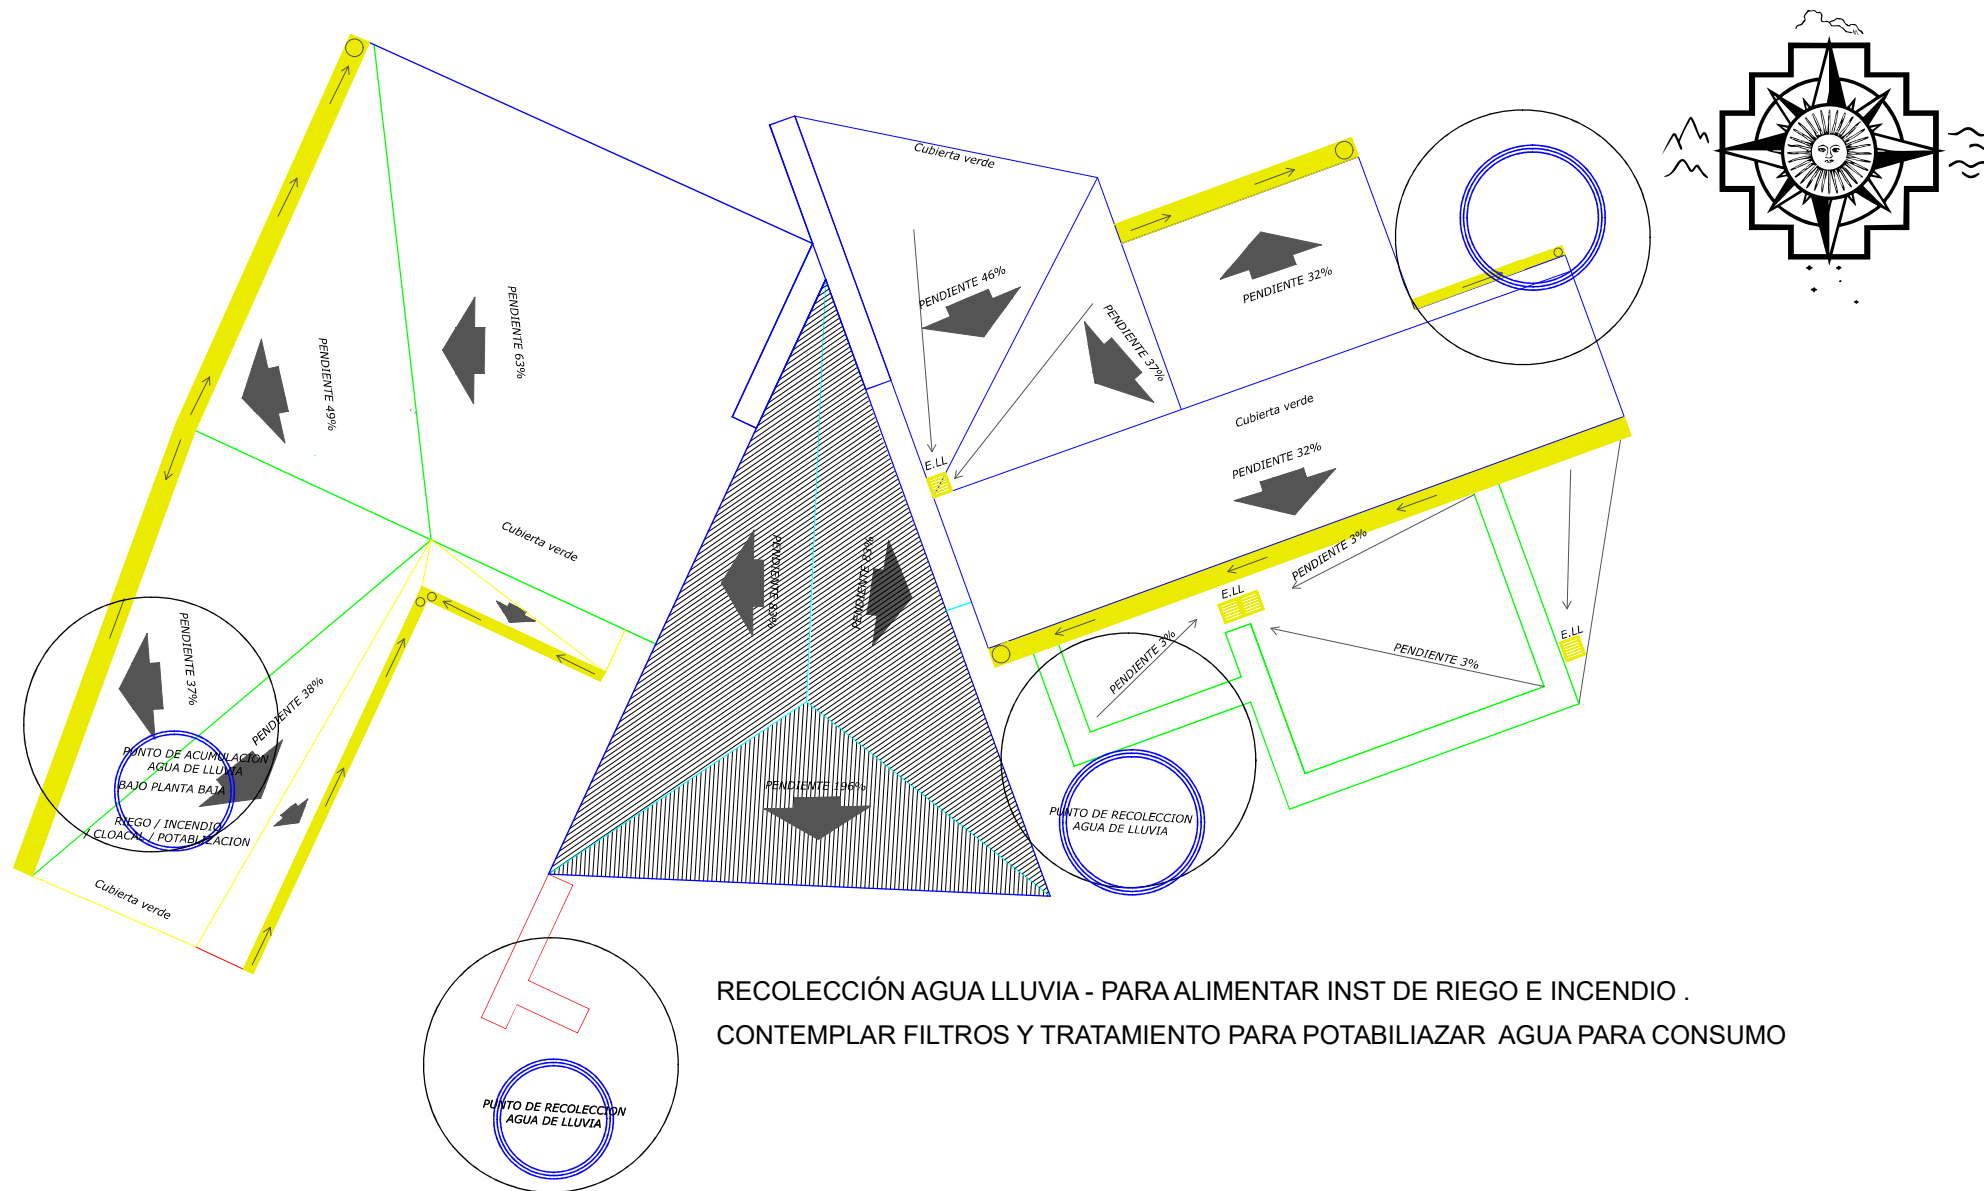


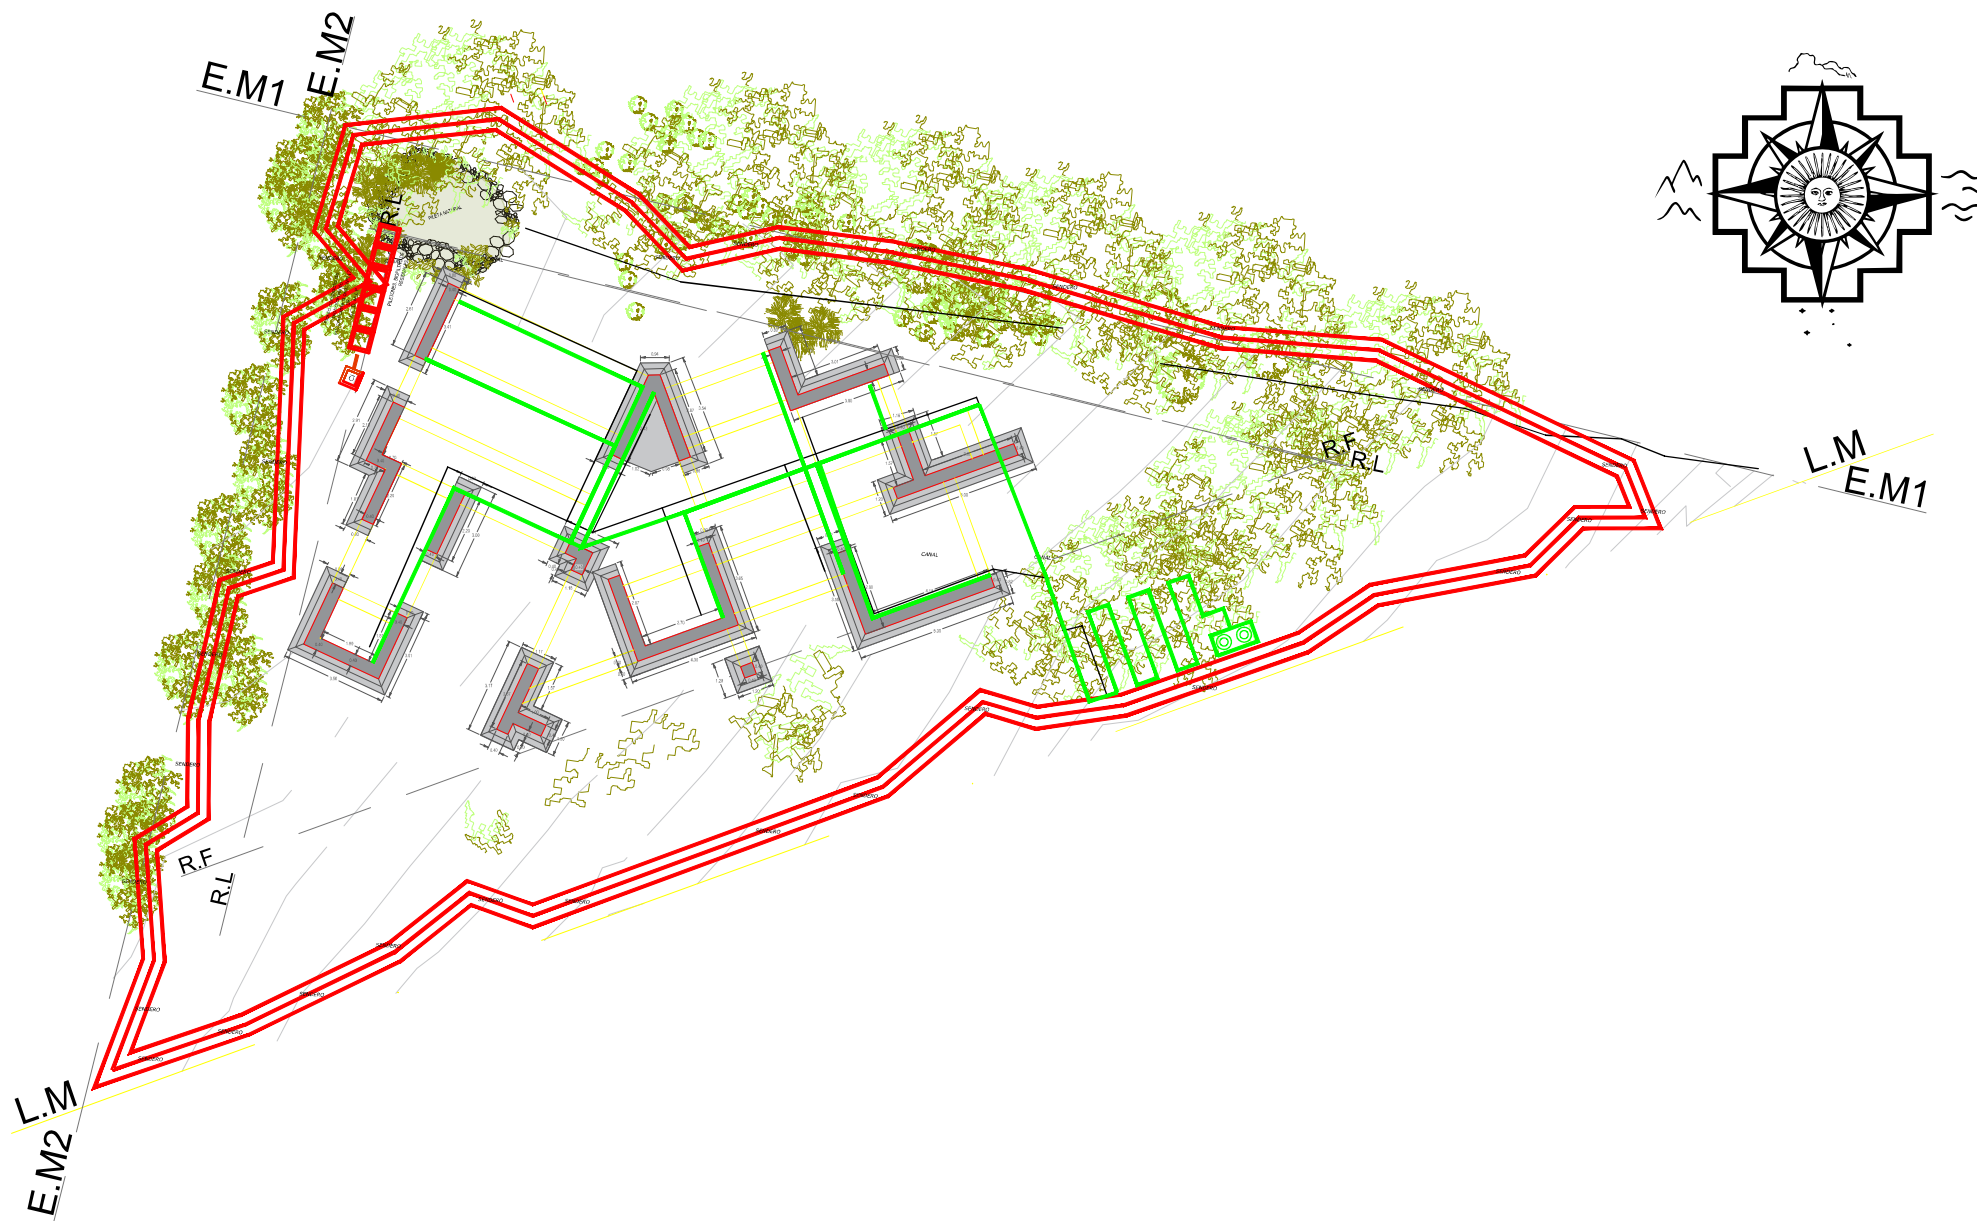





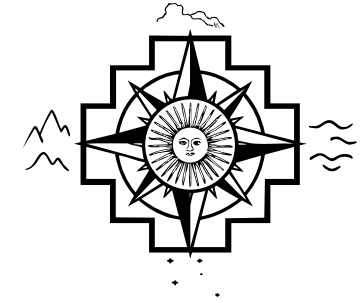


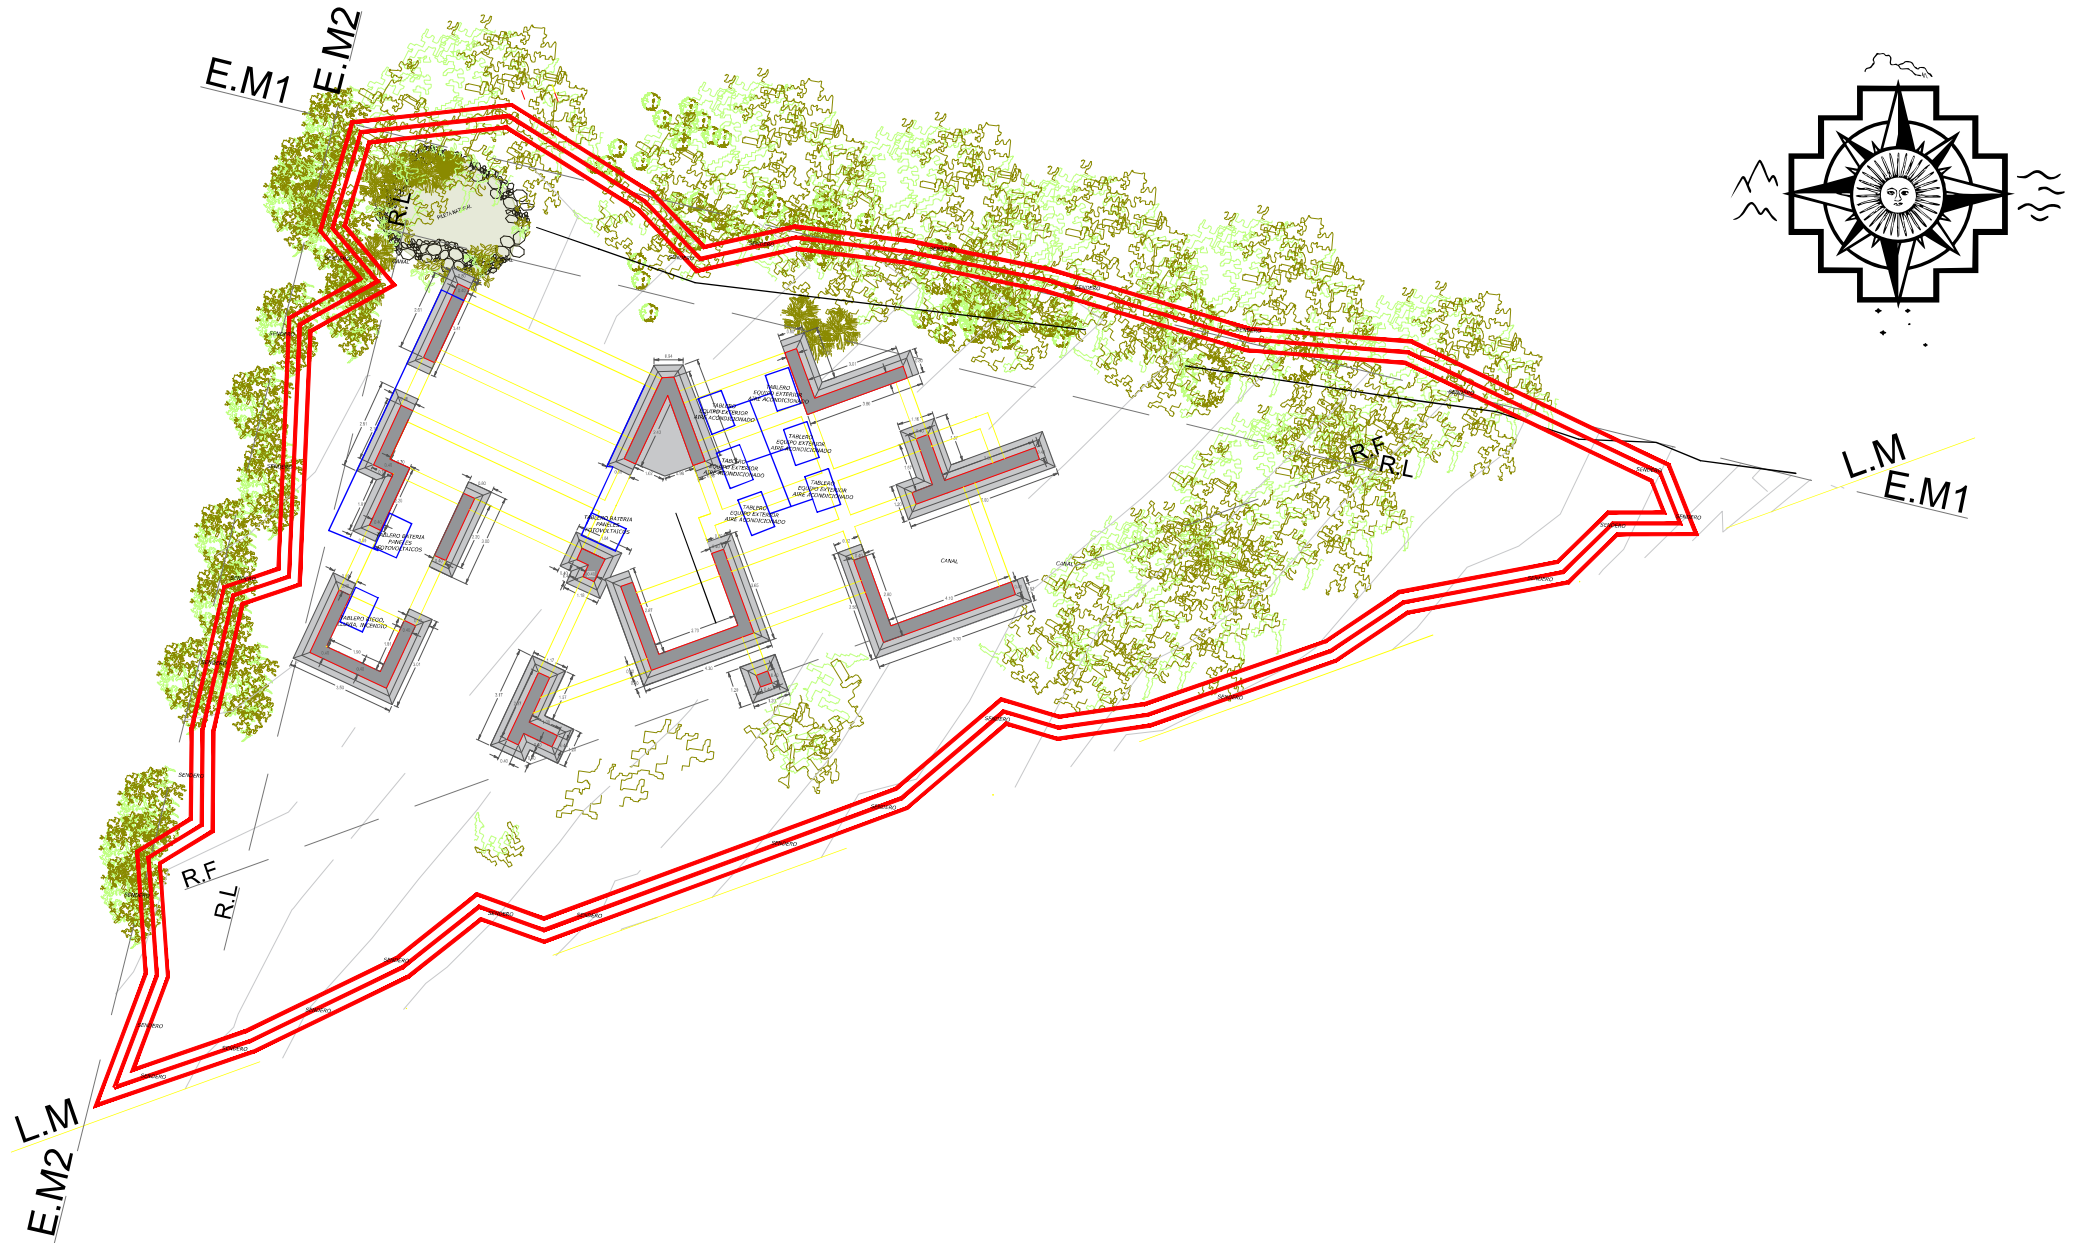

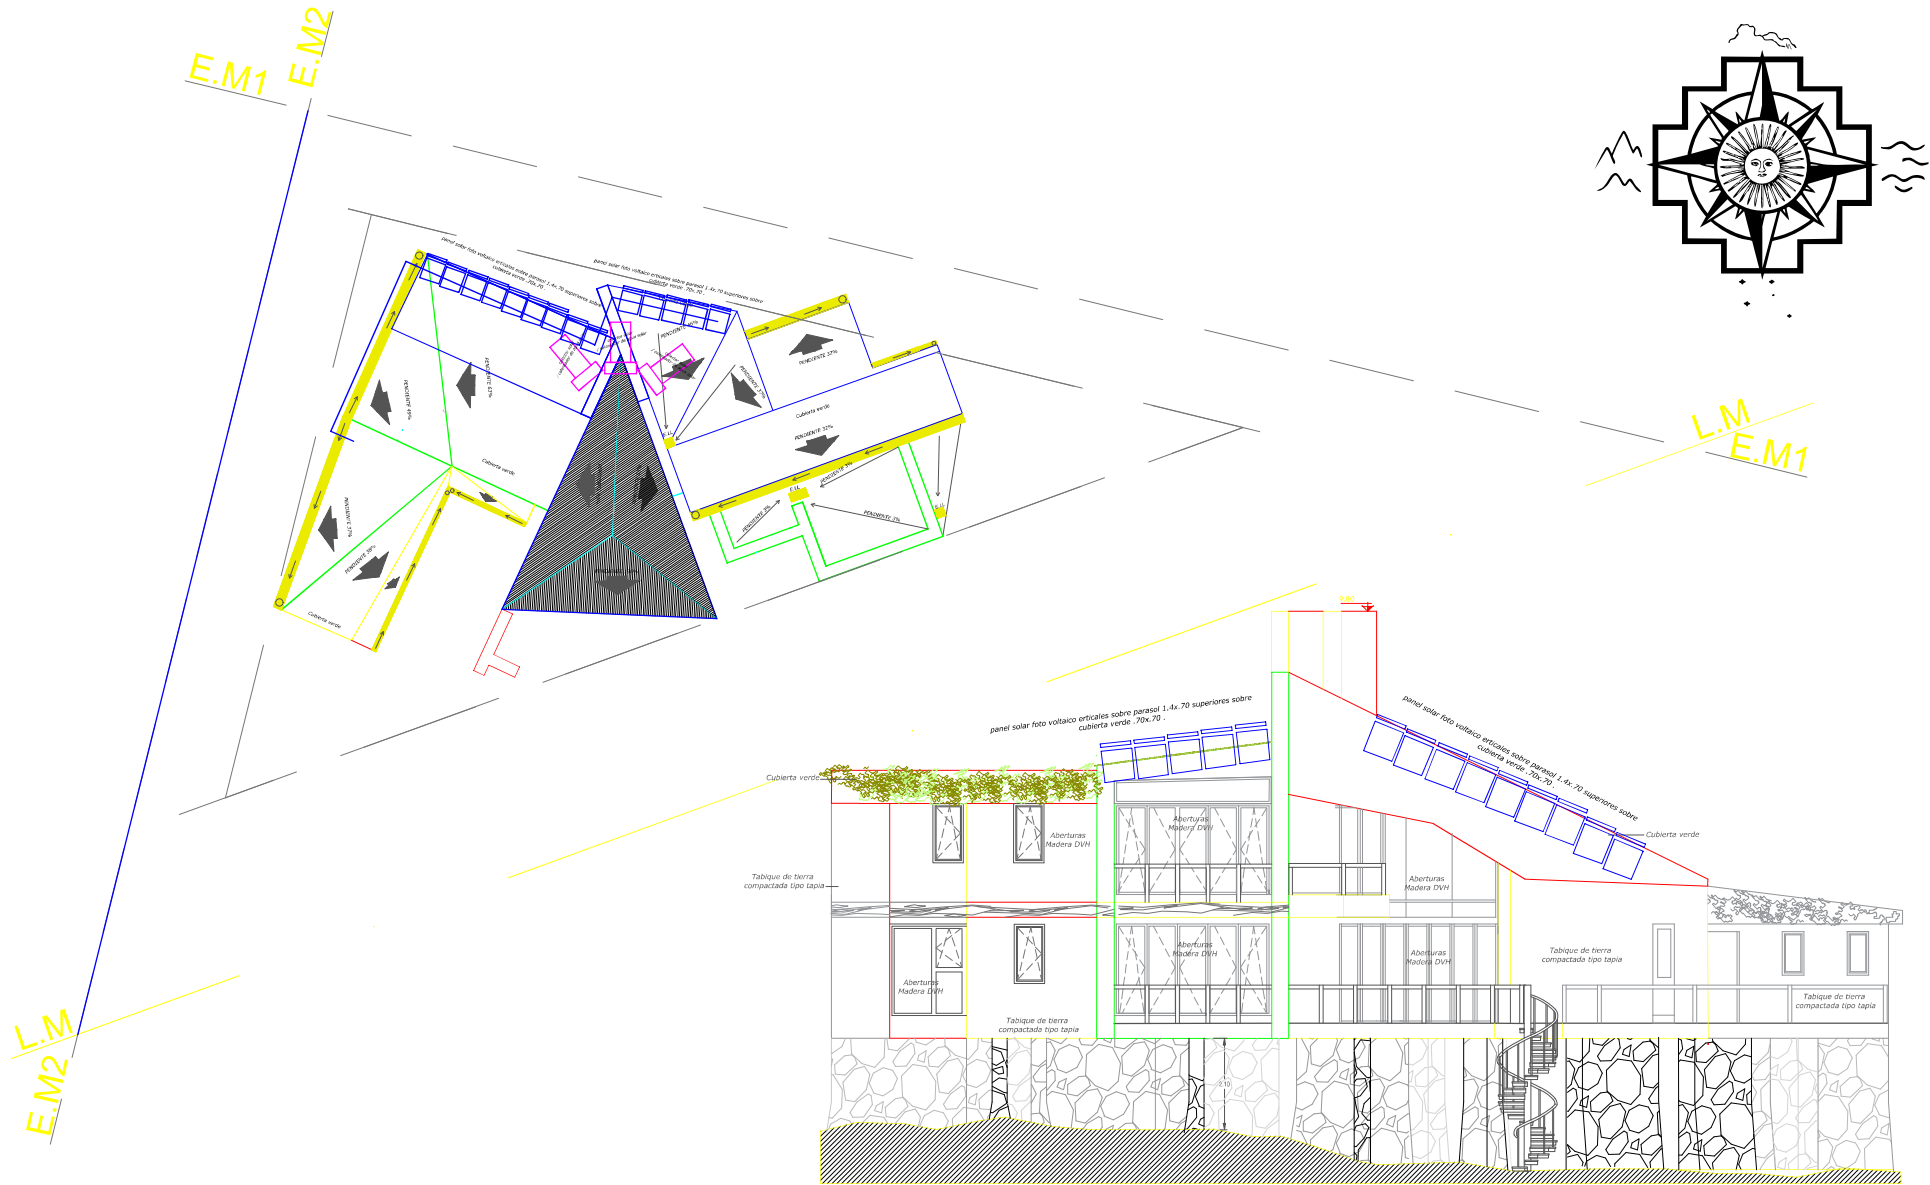


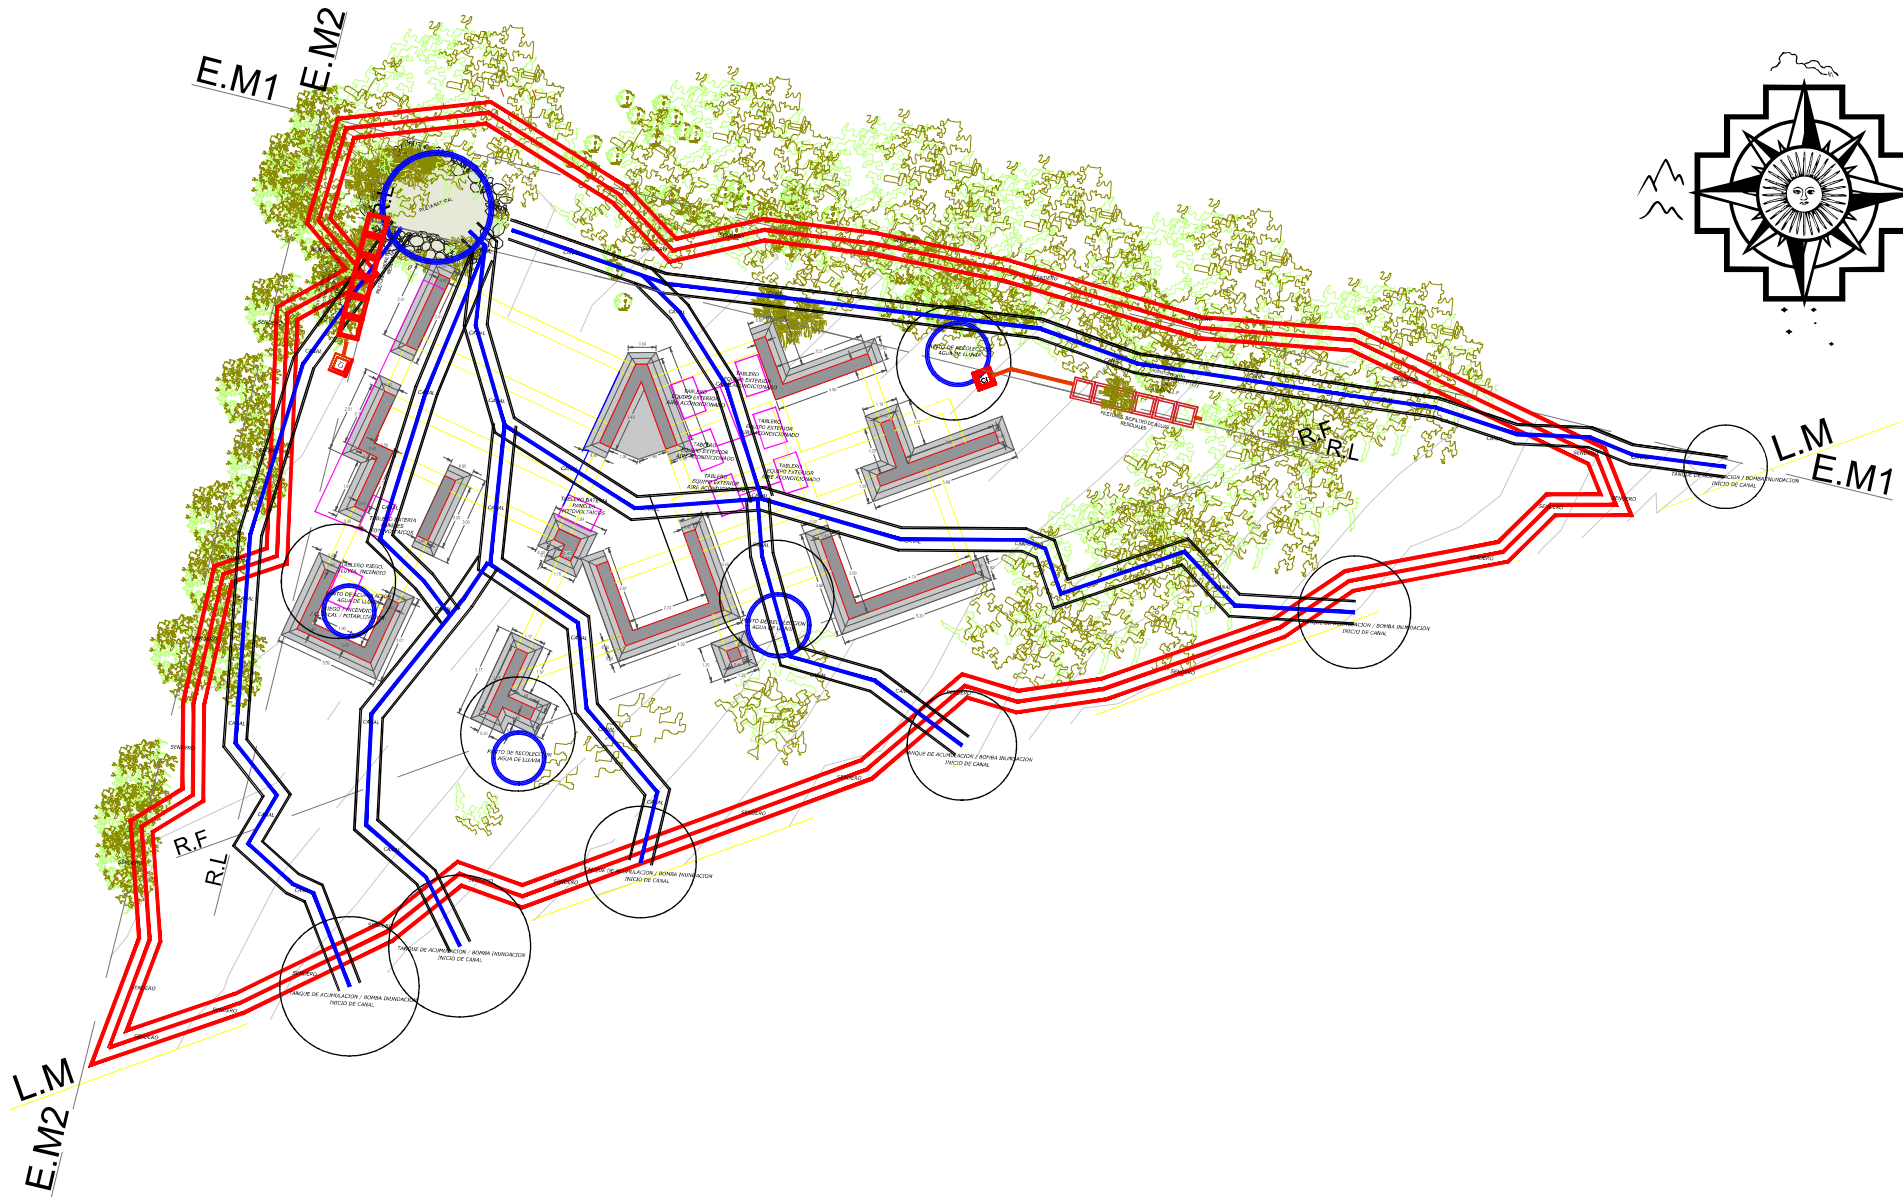

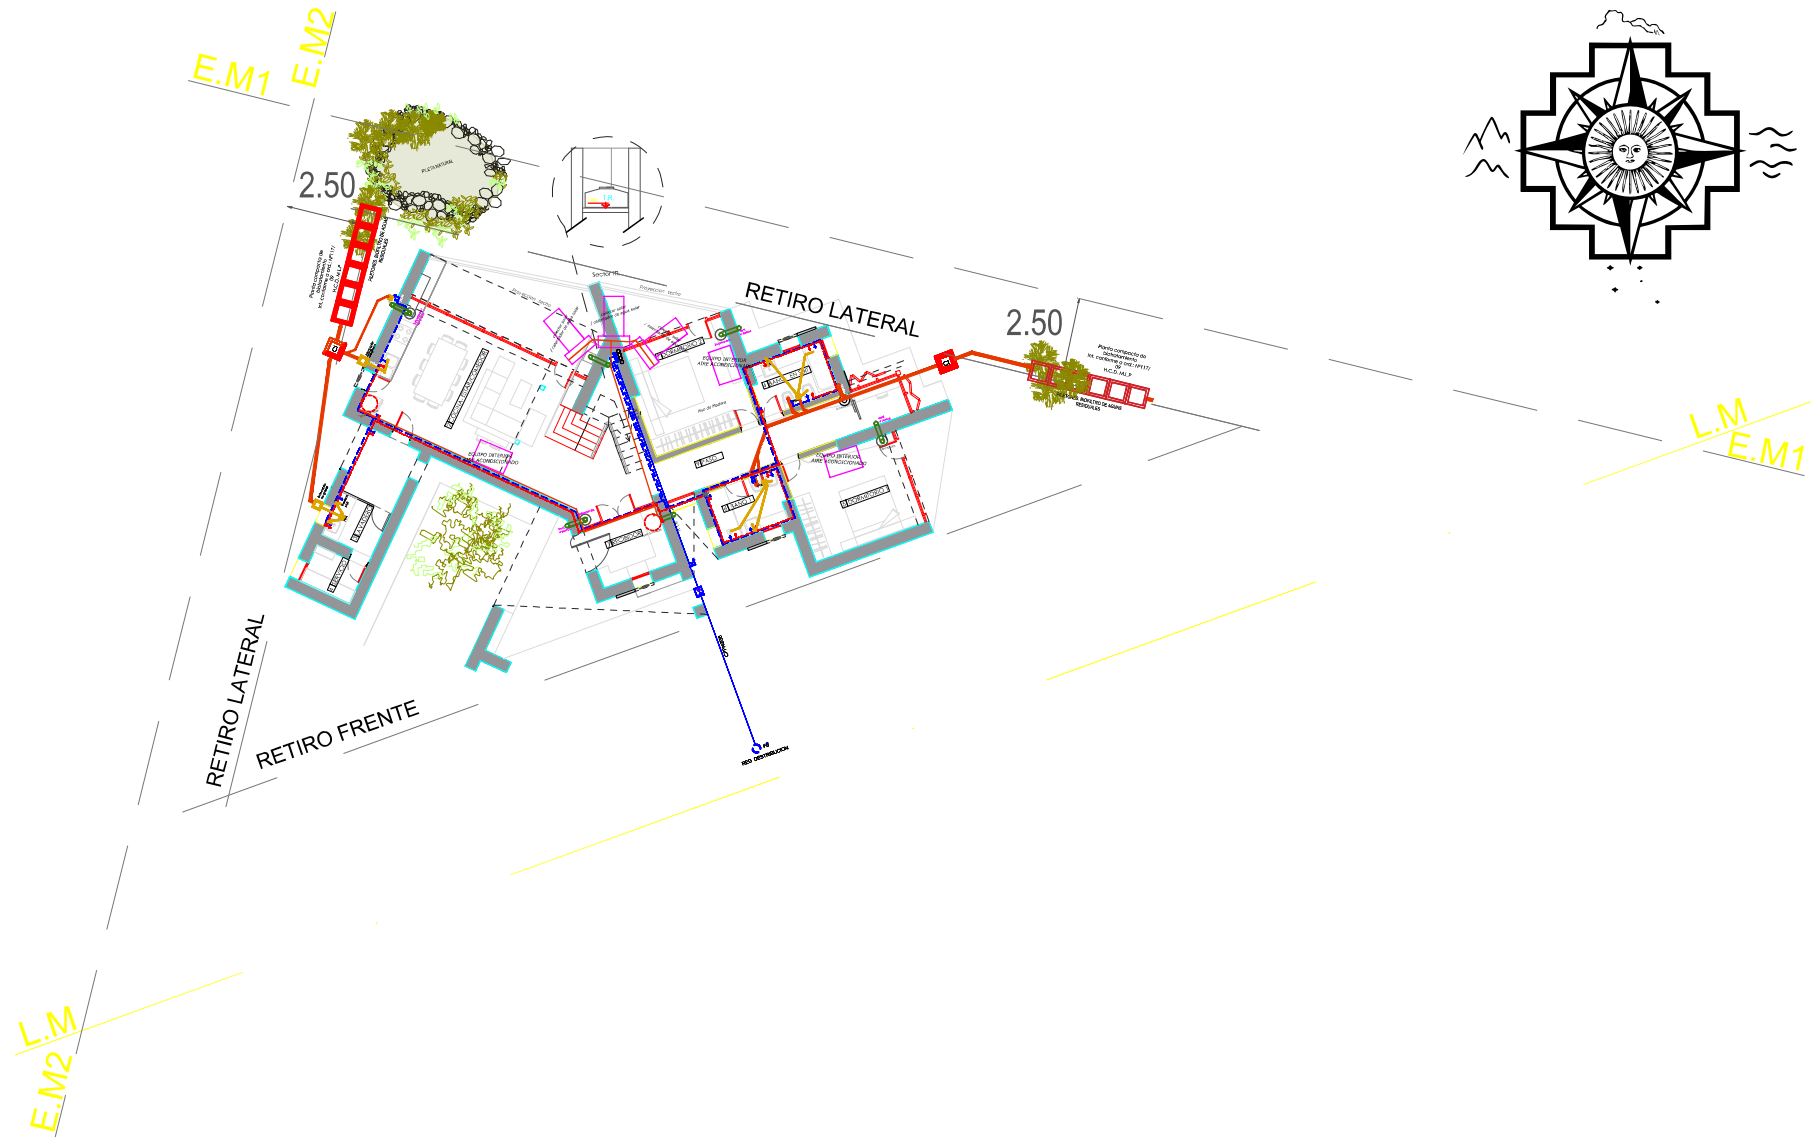

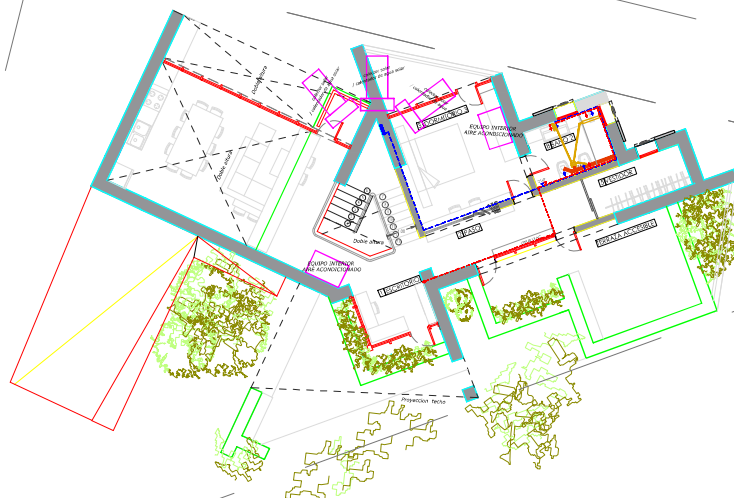

E.M1 E.M

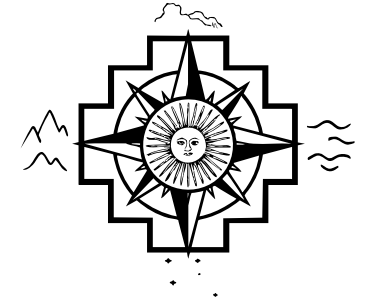

L.M
E.M1

L.M
E.M2

